AP1 (Ch 0+000.0)
AP2(Ch 0+019.0)
AP3(Ch 0+038.0)
AP4(Ch 0+057.0)
AP5 (Ch 0+076.0)
AP6(Ch 0+104.0)
AP7(Ch 0+123.0)
AP8(Ch 0+136.36)
AP9(Ch 0+149.72)
AP10(Ch 0+163.08)
EXISTING TRESTLE AP11
EXISTING TRESTLE AP12
3.80
4.00
2.67
3.50
19.50
SEA
Limit of Sea
BH16
BH14
PROPOSED DUAL CARRIAGEWAY
EXISTING PALM OIL JETTY TO BE REMOVED
07126806
PROPOSED RETAINING WALL AT NEW LANDING
Existing R.C Drain to be relocated
Existing Conc. Drain
Earth Drain
3 Nos. Pipe
N
Limit of

PROPOSED ELEVATED PALM OIL JETTY CROSSING

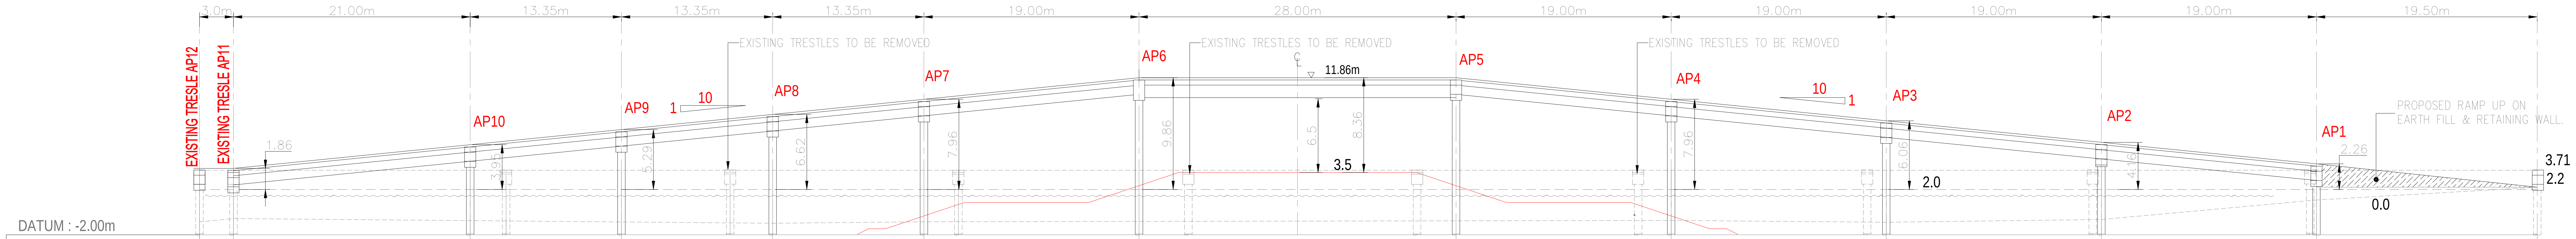
3.0m
21.00m
13.35m
13.35m
13.35m
19.00m
28.00m
19.00m
19.00m
19.00m
19.00m
19.50m
EXISTING TRESLE AP12
EXISTING TRESLE AP11
AP10
AP9
AP8
AP7
AP6
AP5
AP4
AP3
AP2
AP1
EXISTING TRESTLES TO BE REMOVED
EXISTING TRESTLES TO BE REMOVED
EXISTING TRESTLES TO BE REMOVED
1
10
10
1
11.86m
6.5
8.36
3.5
9.86
7.96
6.62
5.29
3.95
1.86
7.96
6.06
2.0
4.16
2.26
PROPOSED RAMP UP ON EARTH FILL & RETAINING WALL.
3.71
2.2
0.0
DATUM : -2.00m

EXISTING LEVEL (m)	-0.860	-0.620				-0.980	-0.850			-0.730	-0.890	-0.650	1.070	2.200
FINISHED LEVEL (m)	3.720	3.710	3.861	5.952	7.288	8.624	9.960	11.860	11.860	9.960	8.060	6.160	4.260	2.200
OFFSET (m)	EXISTING 186.989	183.989	EXISTING	CH 163.08 AP 10	CH149.72 AP 9	CH136.36 AP 8	CH123.00 AP 7	CH104.00 AP 6	CH76.00 AP 5	CH57.00 AP 4	CH38.00 AP 3	CH19.00 AP 2	CH0.00 AP 1	0.00

LONGITUDINAL SECTION

DATE	DESCRIPTION	REFERENCE

REVISION

CONSULTANT :

PJP

PERDANA JURUTERA PERUNDING
2nd Floor, lot 2, Block A, Damai Plaza,
Phase 4, 88300. Kota Kinabalu.
P. O. Box No. 21251, Damai Post Office,
88770. Kota Kinabalu, SABAH, MALAYSIA .

Engineer's Chop :

Engineer's Signature :

DRAWN BY : FM
CHECKED BY : Ir. Tsen Ying Fui
DESIGNED BY : TZJ
SCALE : 1 TO 300
DATE : SEPT 2013

APPROVED BY :

PENGARAH JKR

TIM. PENGARAH JKR

KETUA PENOLONG PENGARAH (JALAN)

JABATAN KERJA RAYA SABAH

JALAN BOKARA BATU SAPI FASA 2, SANDAKAN (4KM DUAL CARRIAGEWAY)

DRAWING TITLE : PROPOSED ELEVATED PALM OIL JETTY CROSSING

DRAWING NO. : PJP/JKR/P157/JTY/01