

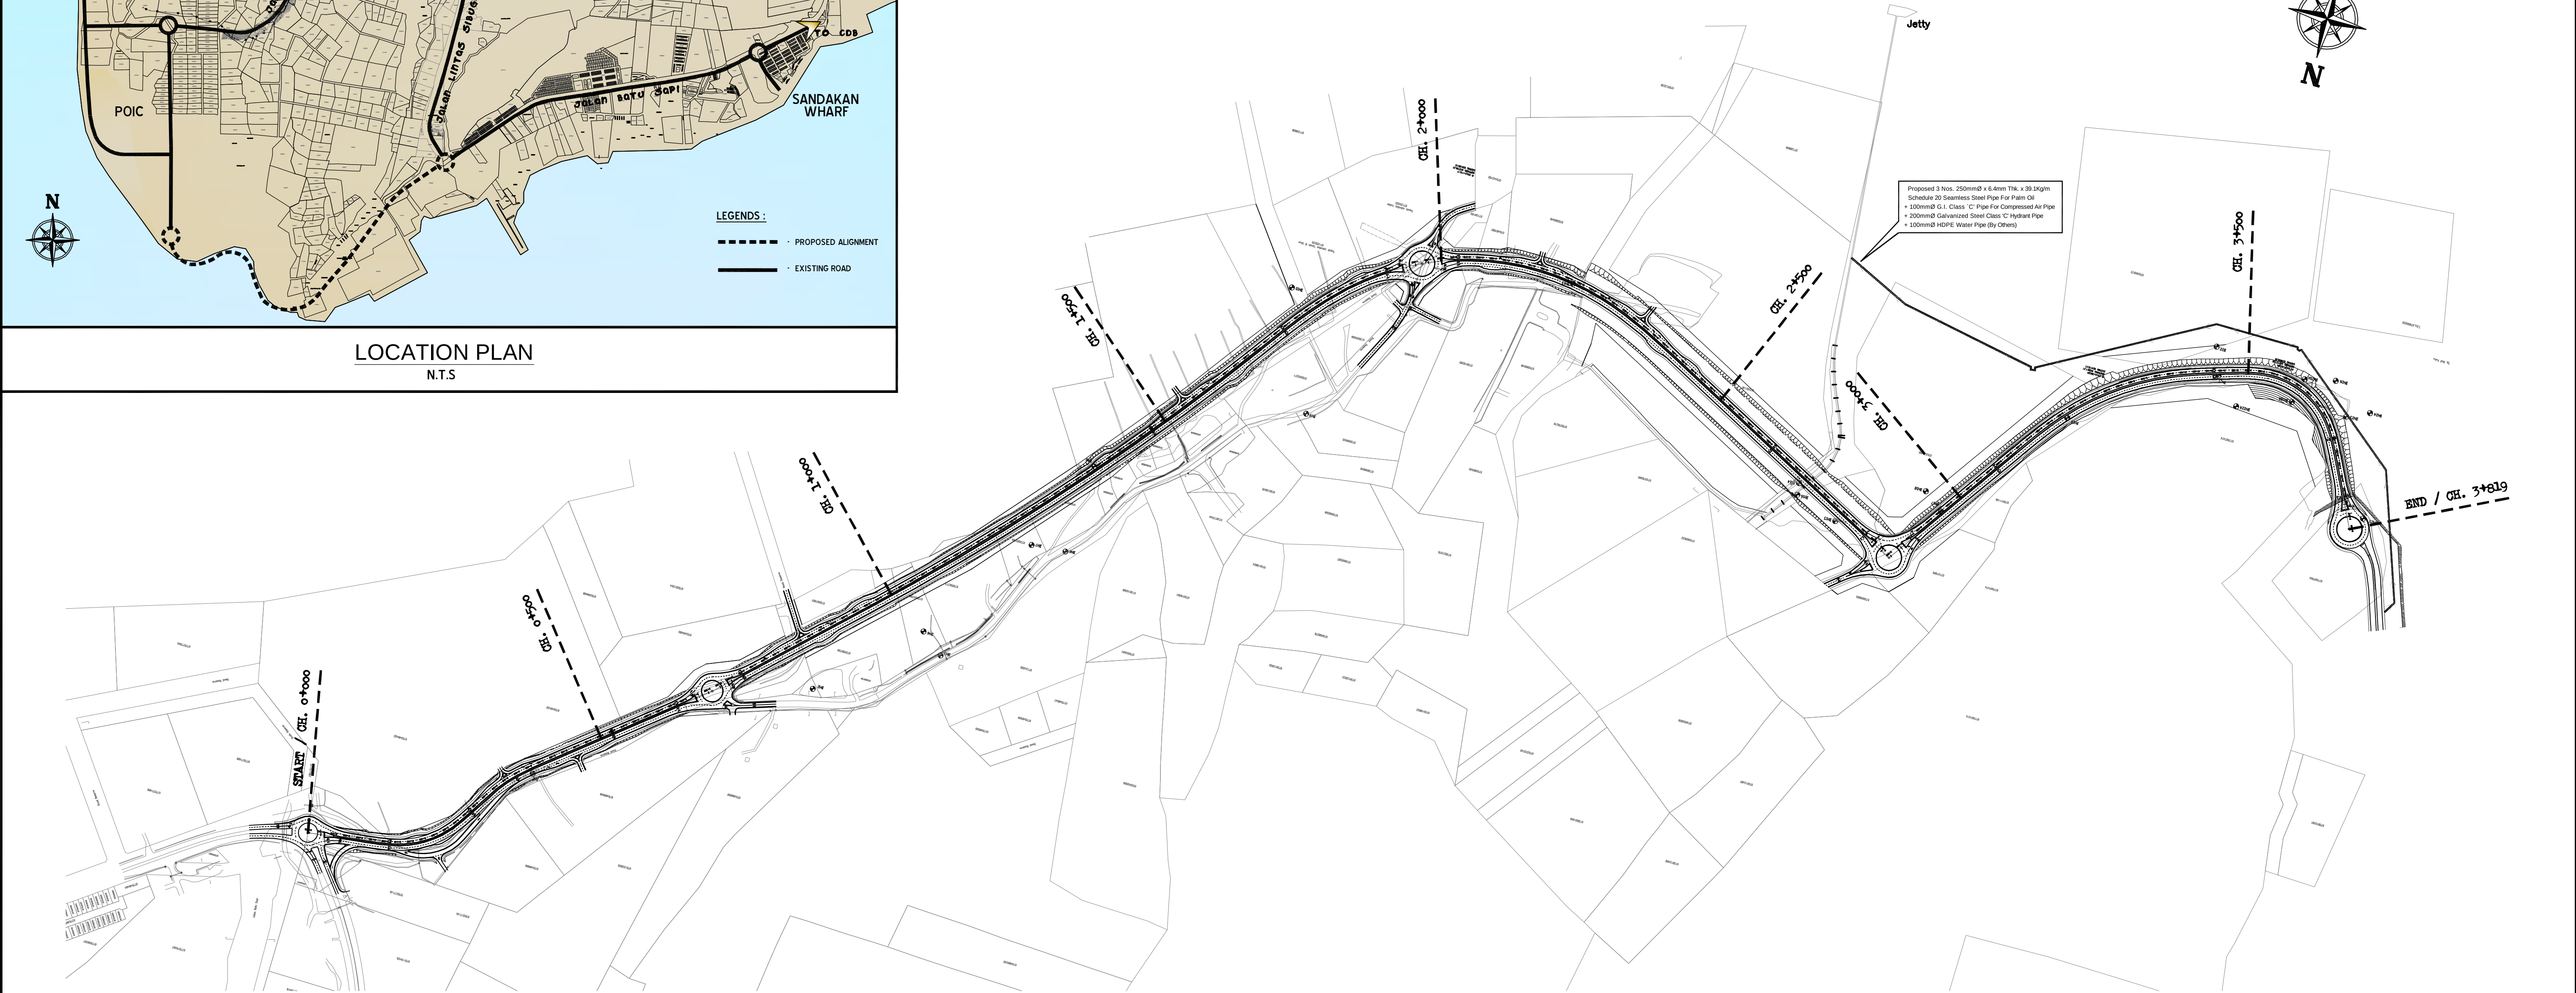


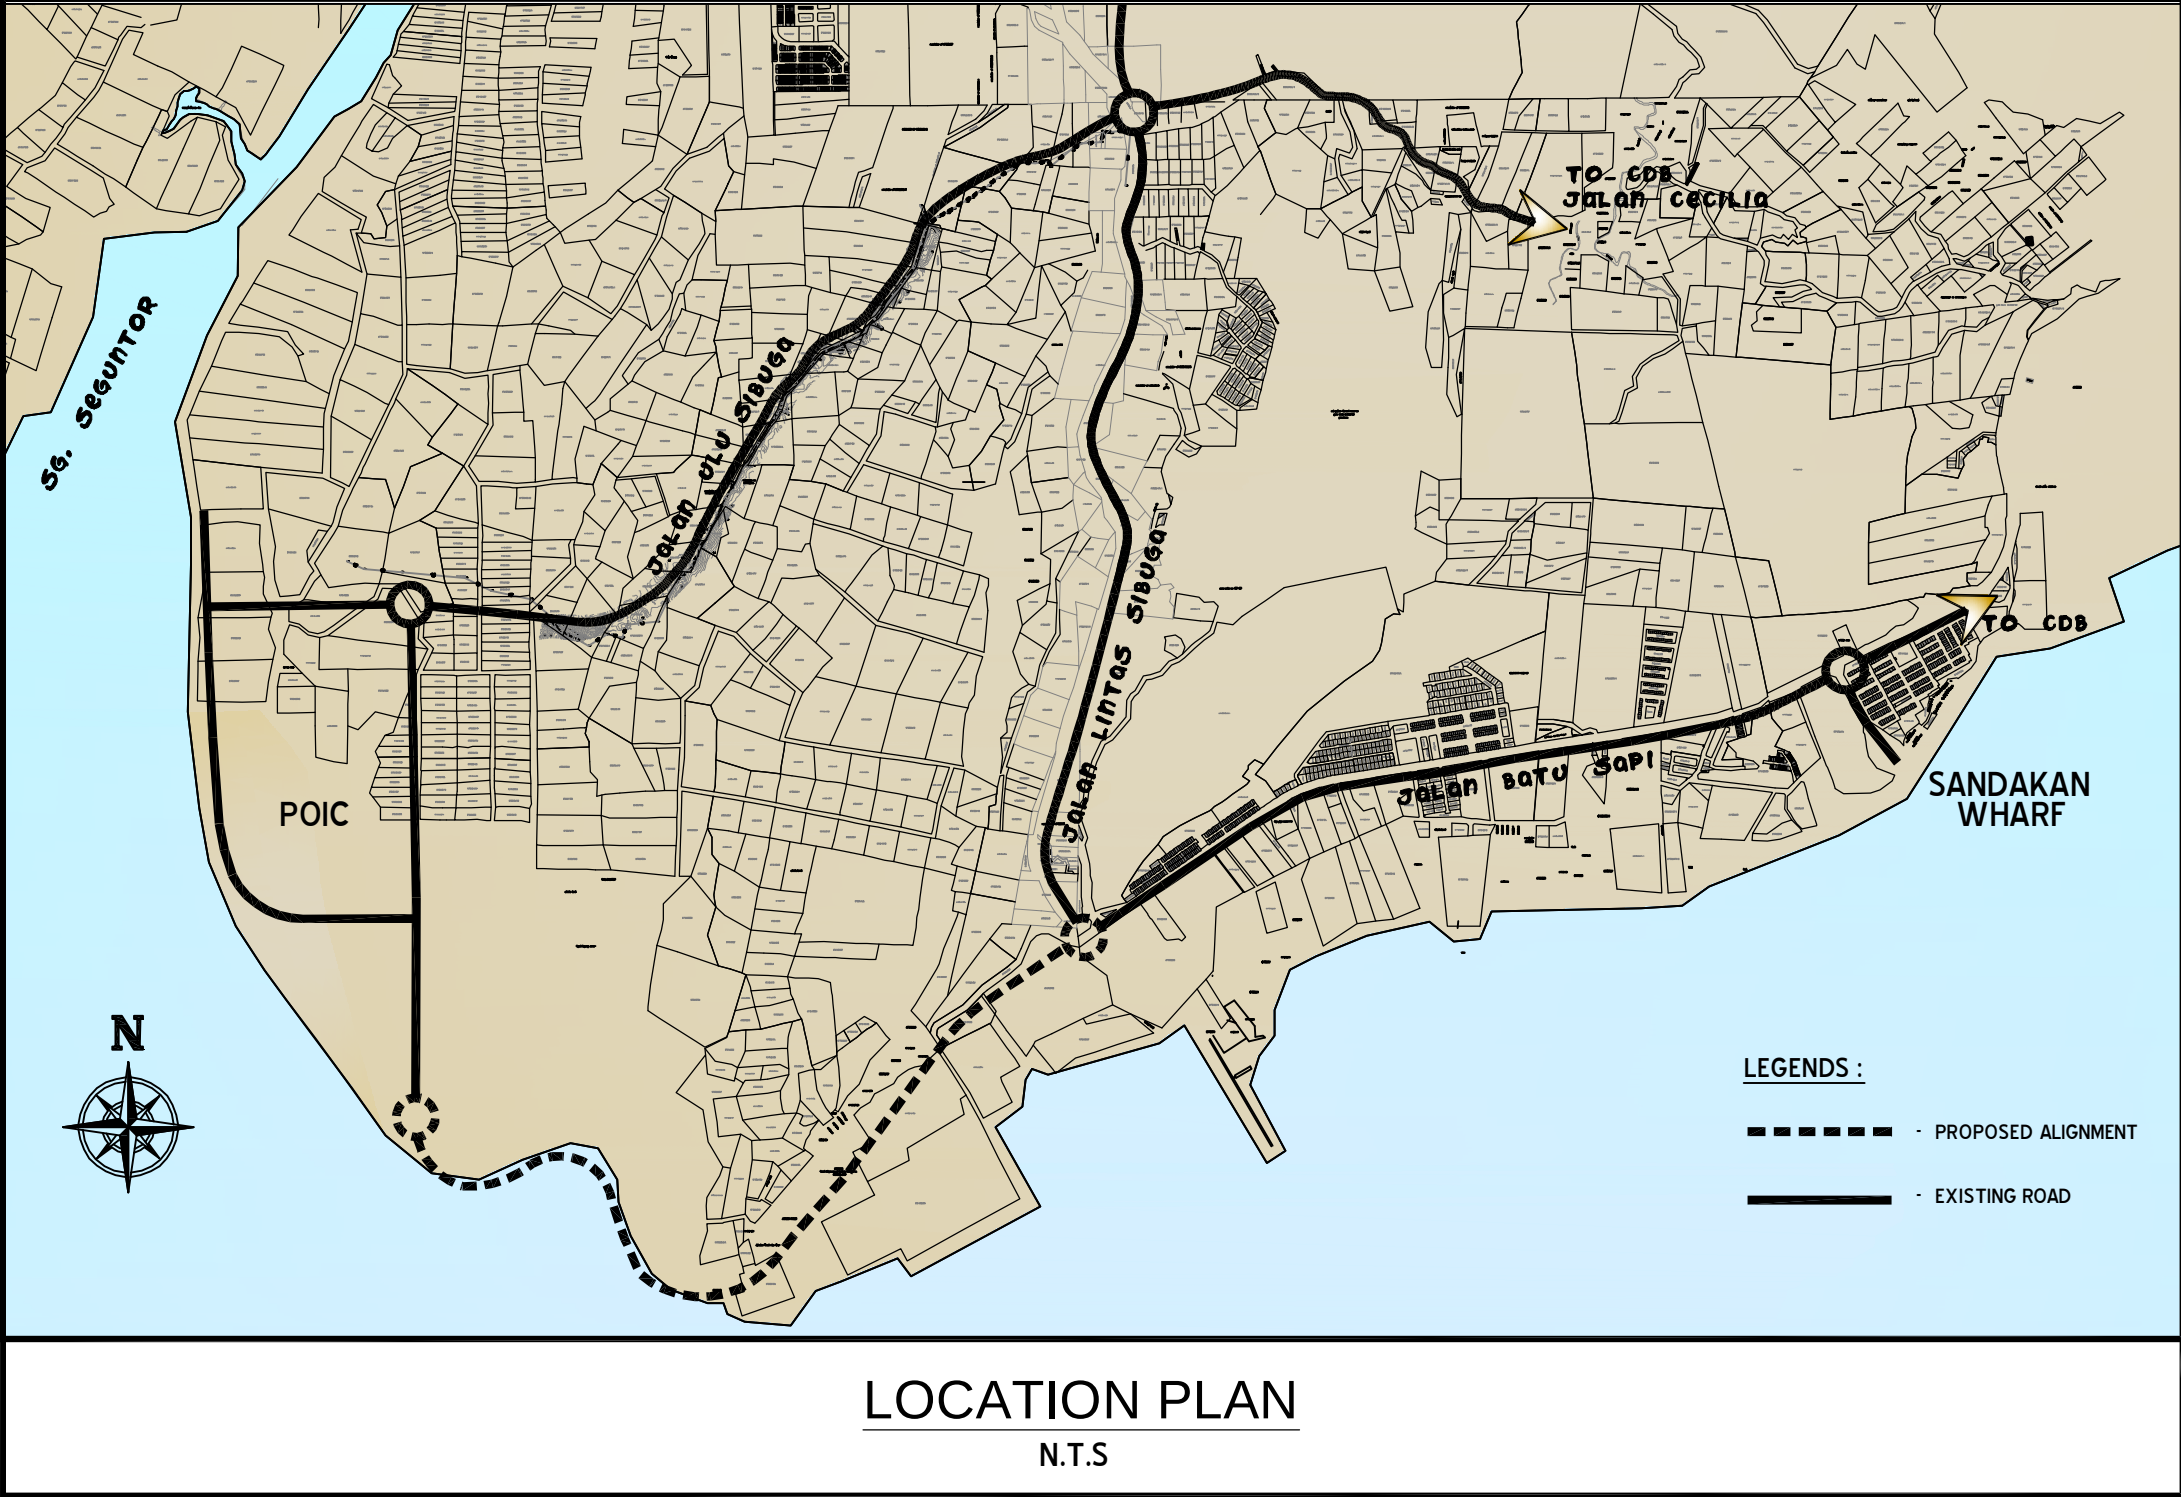

OVERALL HORIZONTAL ALIGNMENT FOR JALAN BOKARA (CH. 0+00 TO CH. 3+819)

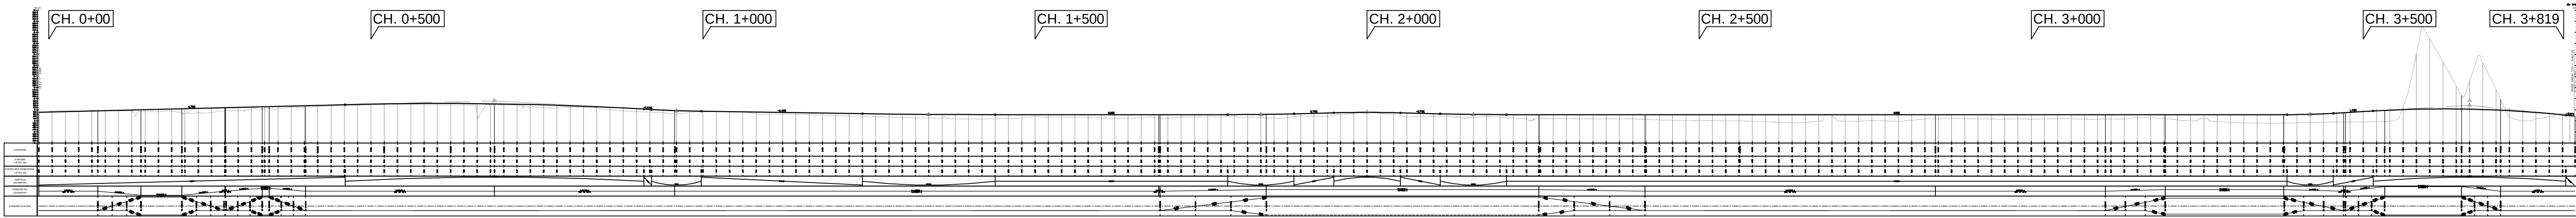

OVERALL VERTICAL ALIGNMENT FOR JALAN BOKARA (CH. 0+00 TO CH. 3+819)

DATE	DESCRIPTION	REFERENCE	CONSULTANT :	Engineer's Chop :	Engineer's Signature :	APPROVED BY :	 JABATAN KERJA RAYA SABAH	
			 PERDANA JURUTERA PERUNDING 2nd Floor, lot 2, Block A, Damai Plaza, Phase 4, 88300, Kota Kinabalu. P. O. Box No. 21251, Damai Post Office, 88770, Kota Kinabalu, SABAH, MALAYSIA .			----- PENGARAH JKR	JALAN BOKARA BATU SAPI FASA 2, SANDAKAN (4KM DUAL CARRIAGEWAY)	
					DRAWN BY : Jonathan / Ben	CHECKED BY : Ir. Lucas Lo	----- TIM. PENGARAH JKR	DRAWING TITLE : SITE LOCATION & OVERALL ALIGNMENT PLAN
					DESIGNED BY : Mohd Erwin N.			
REVISION					SCALE : As Shown	DATE : September 2013	----- KETUA PENOLONG PENGARAH (JALAN)	DRAWING NO. : PJP/P157/GE/01