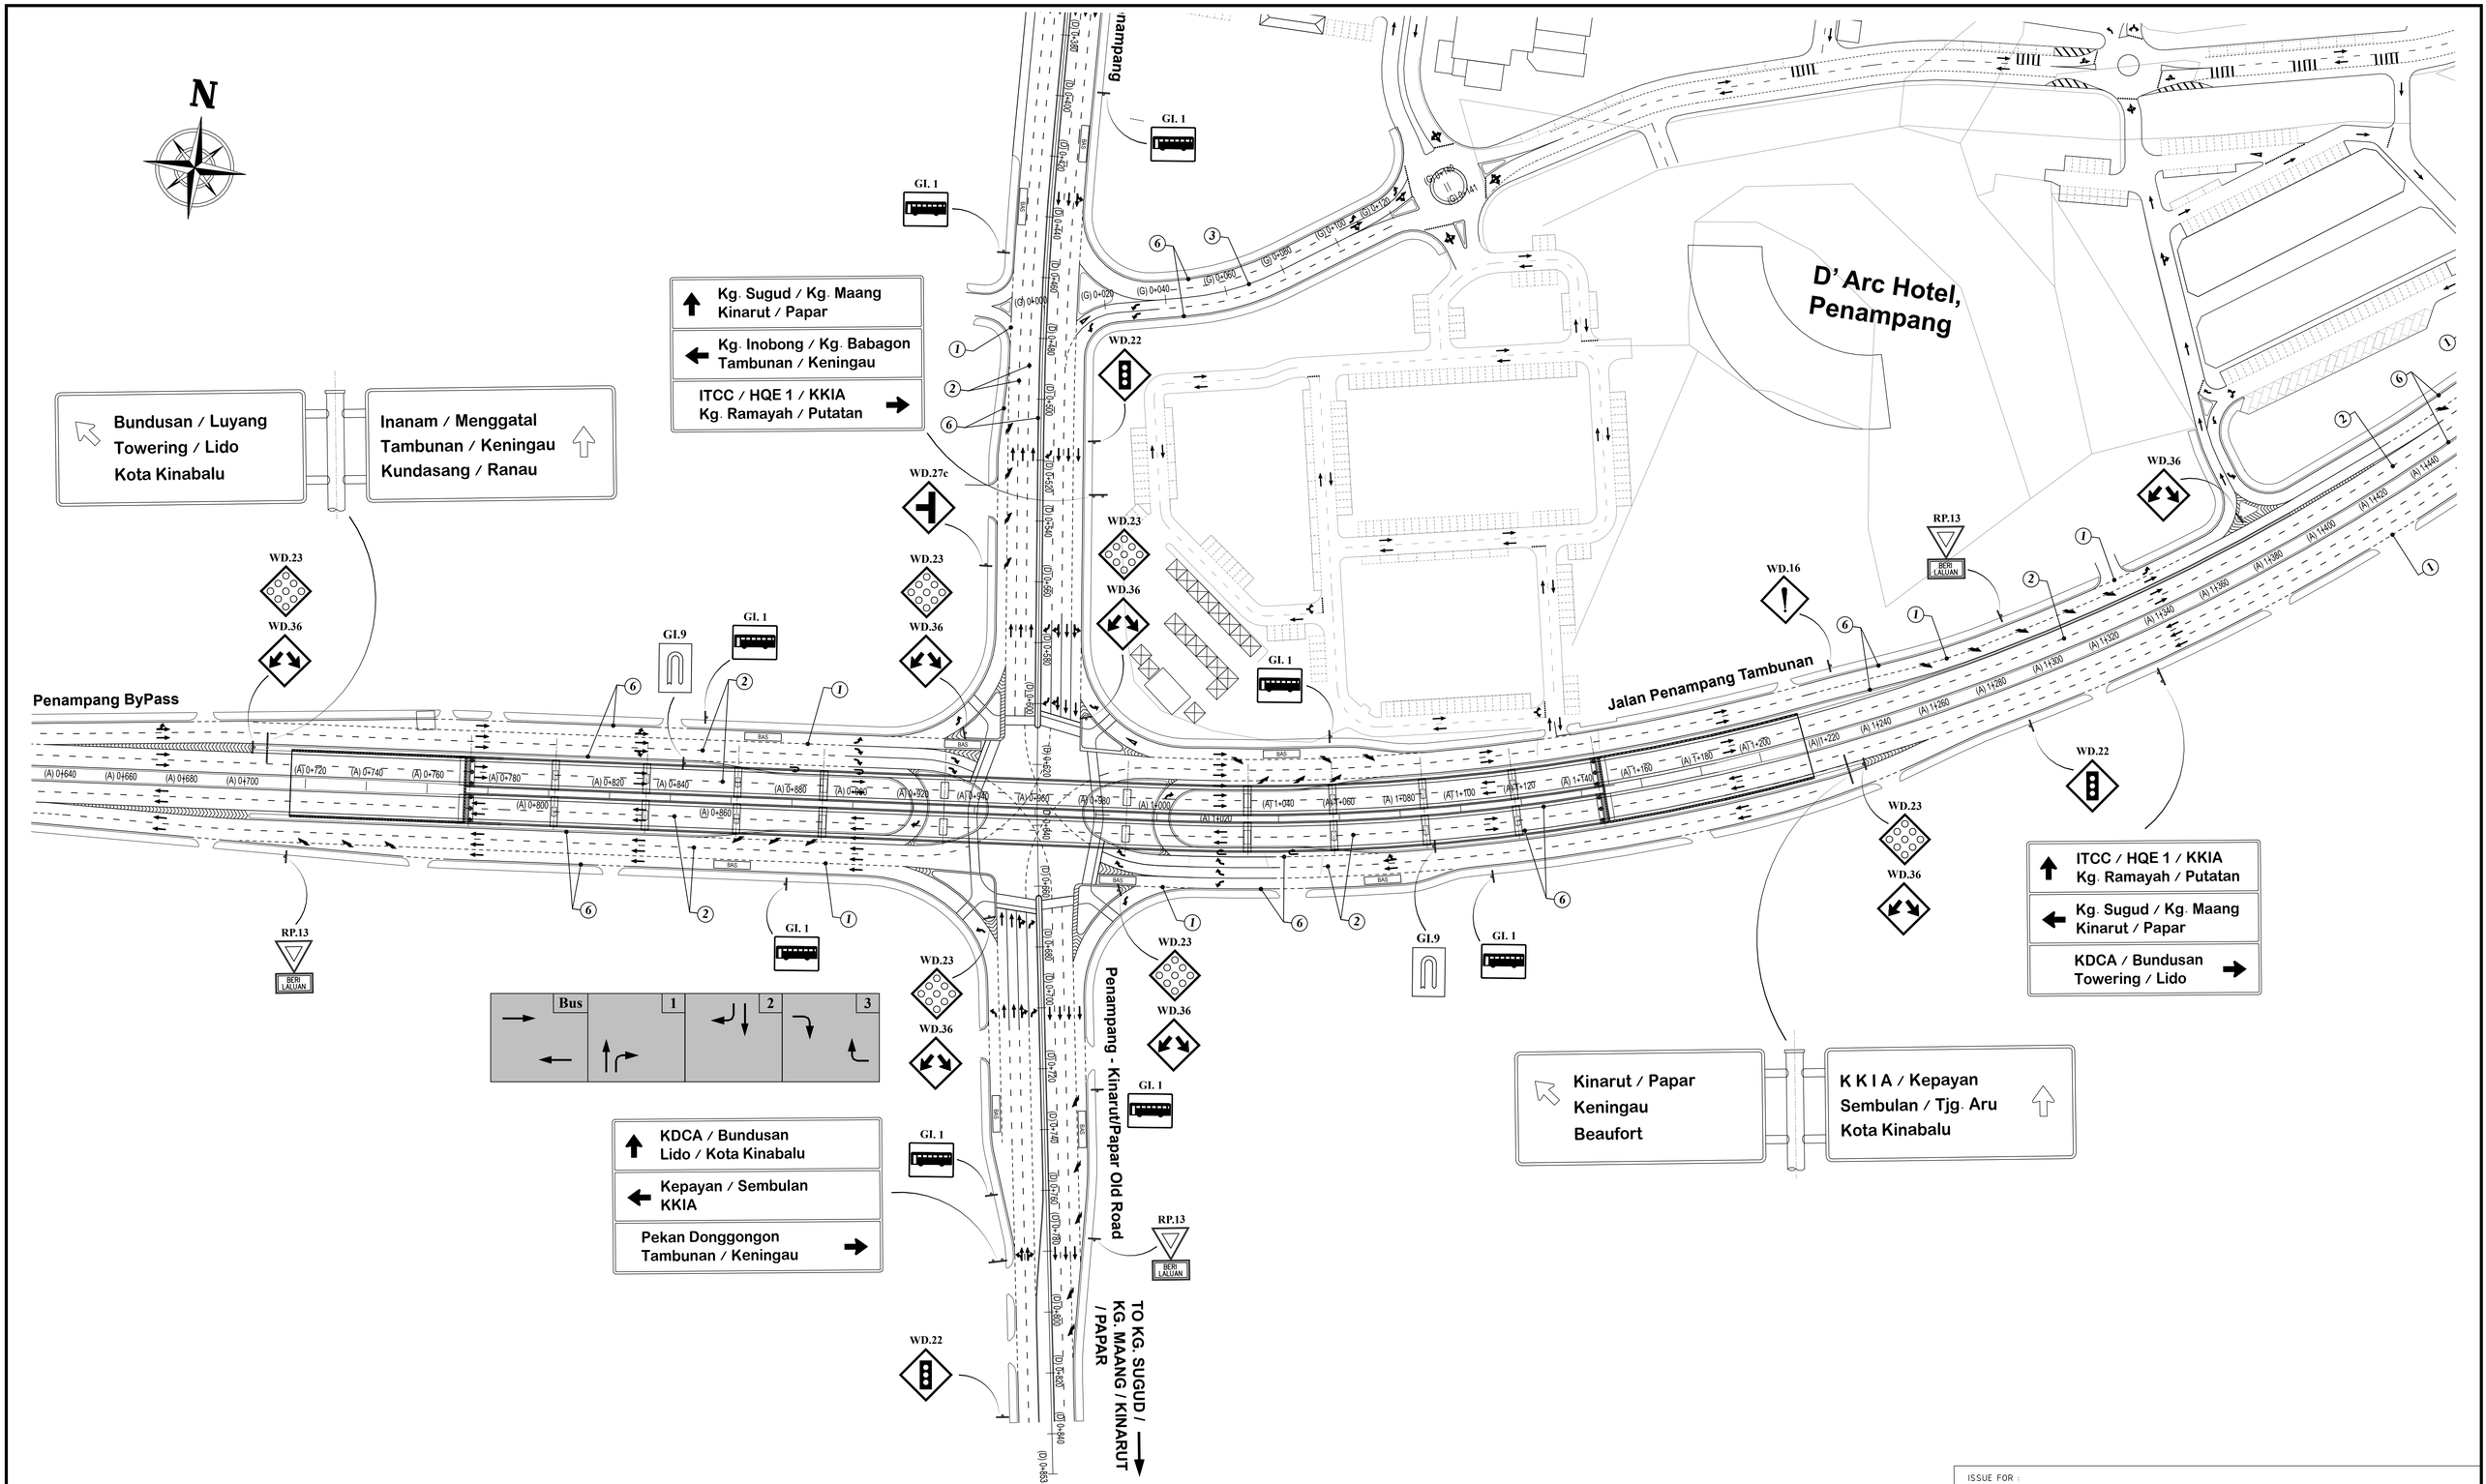

DATE	DESCRIPTION	REV.

CONSULTING ENGINEERS:

PJP

PERDANA JURUTERA PERUNDING

3rd Floor, Lot 34 & 35, Block E, Damai Plaza,
Phase 4, 88300 Kota Kinabalu, Sabah.
P. O. Box 21251, Damai Post Office,
88770 Kota Kinabalu, Sabah.

Lead Engineer:

Design Engineer:

DRAWN BY	**Jonathan Abah**
DESIGNED BY	**George CSK**
CHECKED BY	**Ir. Lucas Lo**
SCALE	**H = 1 : 1 000**
DATE	**June 2021**

SUPERINTENDING OFFICER:

JKR SABAH

JABATAN KERJA RAYA
SABAH

Approved by:

Pengarah Kerja Raya

OWNER :

KEMENTERIAN
KERJA RAYA
MALAYSIA

ISSUE FOR :

PROJECT TITLE :

**MENAIK TARAF JALAN DONGGONGON - TAMBUNAN (R500)
DARI PERSIMPANGAN ITCC KE PERSIMPANGAN
JALAN DATUK PANGLIMA BANTING, PENAMPANG, SABAH.**

DRAWING TITLE :

PROPOSED ROAD MARKING & SIGNAGES - LAYOUT (02)

DRAWING NO.

KPKR / J / R / 10 / 2020 / 65 / RMF / 02

REV.