



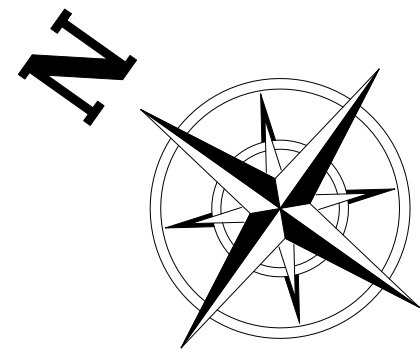

TAMAN TUN FUAD

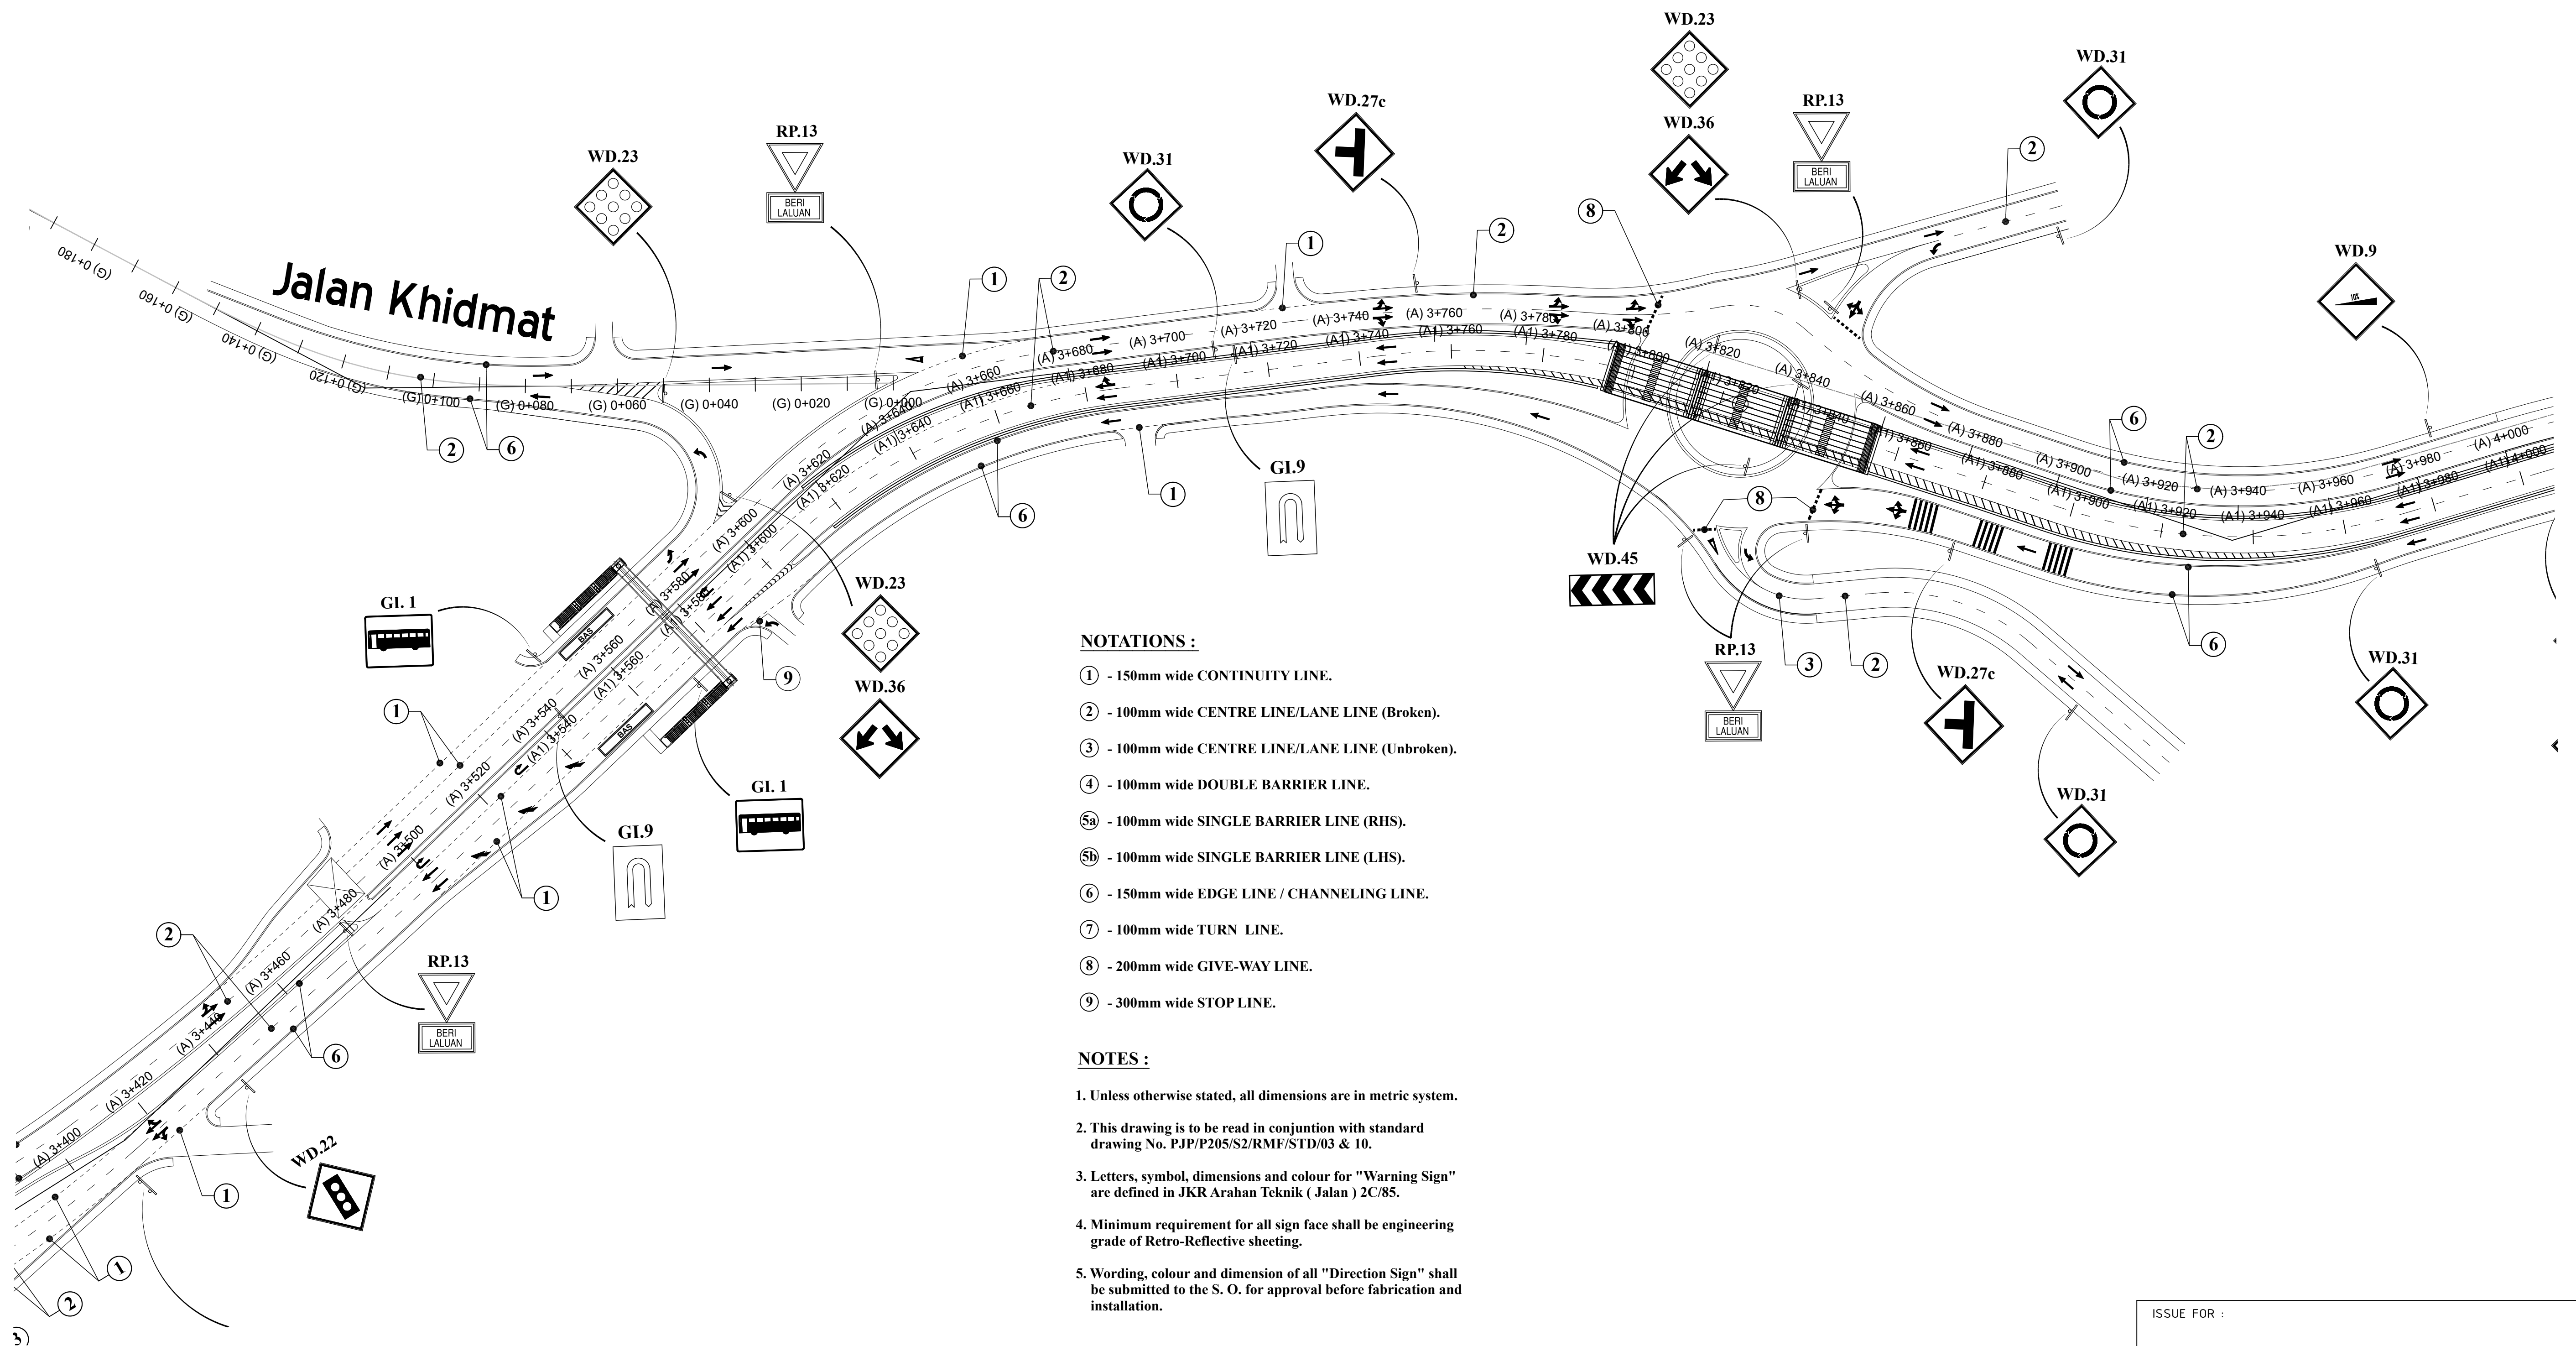


NOTATIONS :

- ① - 150mm wide CONTINUITY LINE.
- ② - 100mm wide CENTRE LINE/LANE LINE (Broken).
- ③ - 100mm wide CENTRE LINE/LANE LINE (Unbroken).
- ④ - 100mm wide DOUBLE BARRIER LINE.
- ⑤a - 100mm wide SINGLE BARRIER LINE (RHS).
- ⑤b - 100mm wide SINGLE BARRIER LINE (LHS).
- ⑥ - 150mm wide EDGE LINE / CHANNELING LINE.
- ⑦ - 100mm wide TURN LINE.
- ⑧ - 200mm wide GIVE-WAY LINE.
- ⑨ - 300mm wide STOP LINE.

NOTES :

1. Unless otherwise stated, all dimensions are in metric system.
2. This drawing is to be read in conjunction with standard drawing No. PJP/P205/S2/RMF/STD/03 & 10.
3. Letters, symbol, dimensions and colour for "Warning Sign" are defined in JKR Arahan Teknik (Jalan) 2C/85.
4. Minimum requirement for all sign face shall be engineering grade of Retro-Reflective sheeting.
5. Wording, colour and dimension of all "Direction Sign" shall be submitted to the S. O. for approval before fabrication and installation.

DATE			DESCRIPTION			REV.			ISSUE FOR :		
									PROJECT TITLE :		
									PROPOSED UPGRADING OF JALAN KOLAM, KOTA KINABALU (6 KM) INCLUDING TWO (2) FLYOVERS.		
									DRAWING TITLE :		
									PROPOSED ROAD MARKING AND SIGNAGES		
									DRAWING NO.		
									PJP / P205 / S2 / RF / 09		
									REV.		

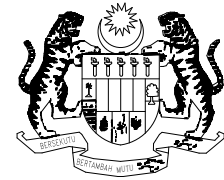CONSULTING ENGINEERS:			DRAWN BY			SUPERINTENDING OFFICER:			OWNER :		
PJP			Jonathan Abah								
Lead Engineer:			DESIGNED BY			Approved by:			KEMENTERIAN		
			George Chin						KERJA RAYA		
Design Engineer:			CHECKED BY			Pengaruh Kerja Raya			MALAYSIA		
			Ir. Lucas Lo								
			SCALE								
			1 : 750 (A1)								
			DATE								
			January 2019								

PERDANA JURUTERA PERUNDING			JABATAN KERJA RAYA			KOTA KINABALU		
3rd Floor, Lot 34 & 35, Block E, Damai Plaza,			SABAH					
Phase 4, 88300, Kota Kinabalu.								
P. O. Box No. 21251, Damai Post Office,								
88770, Kota Kinabalu, SABAH, MALAYSIA.								