



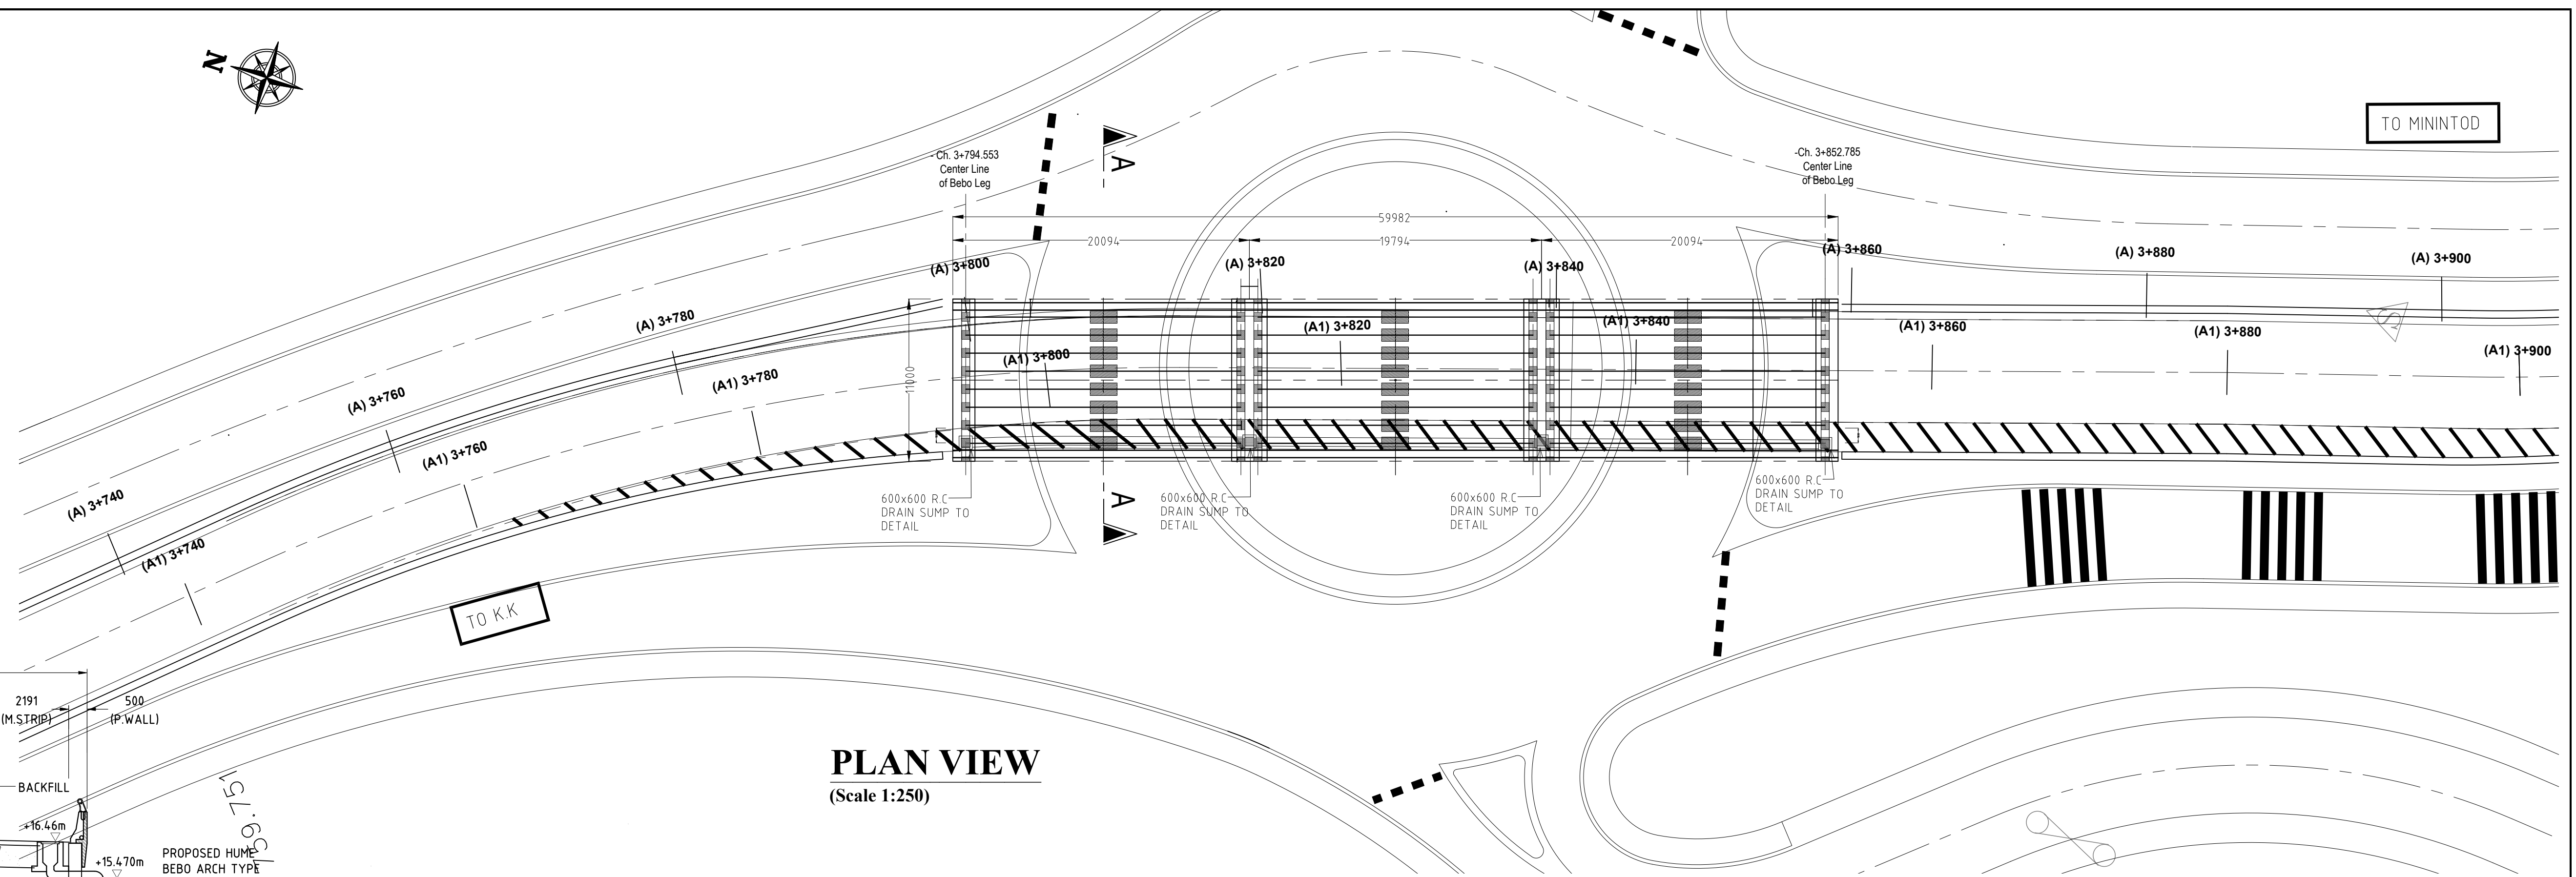


PLAN VIEW

(Scale 1:250)

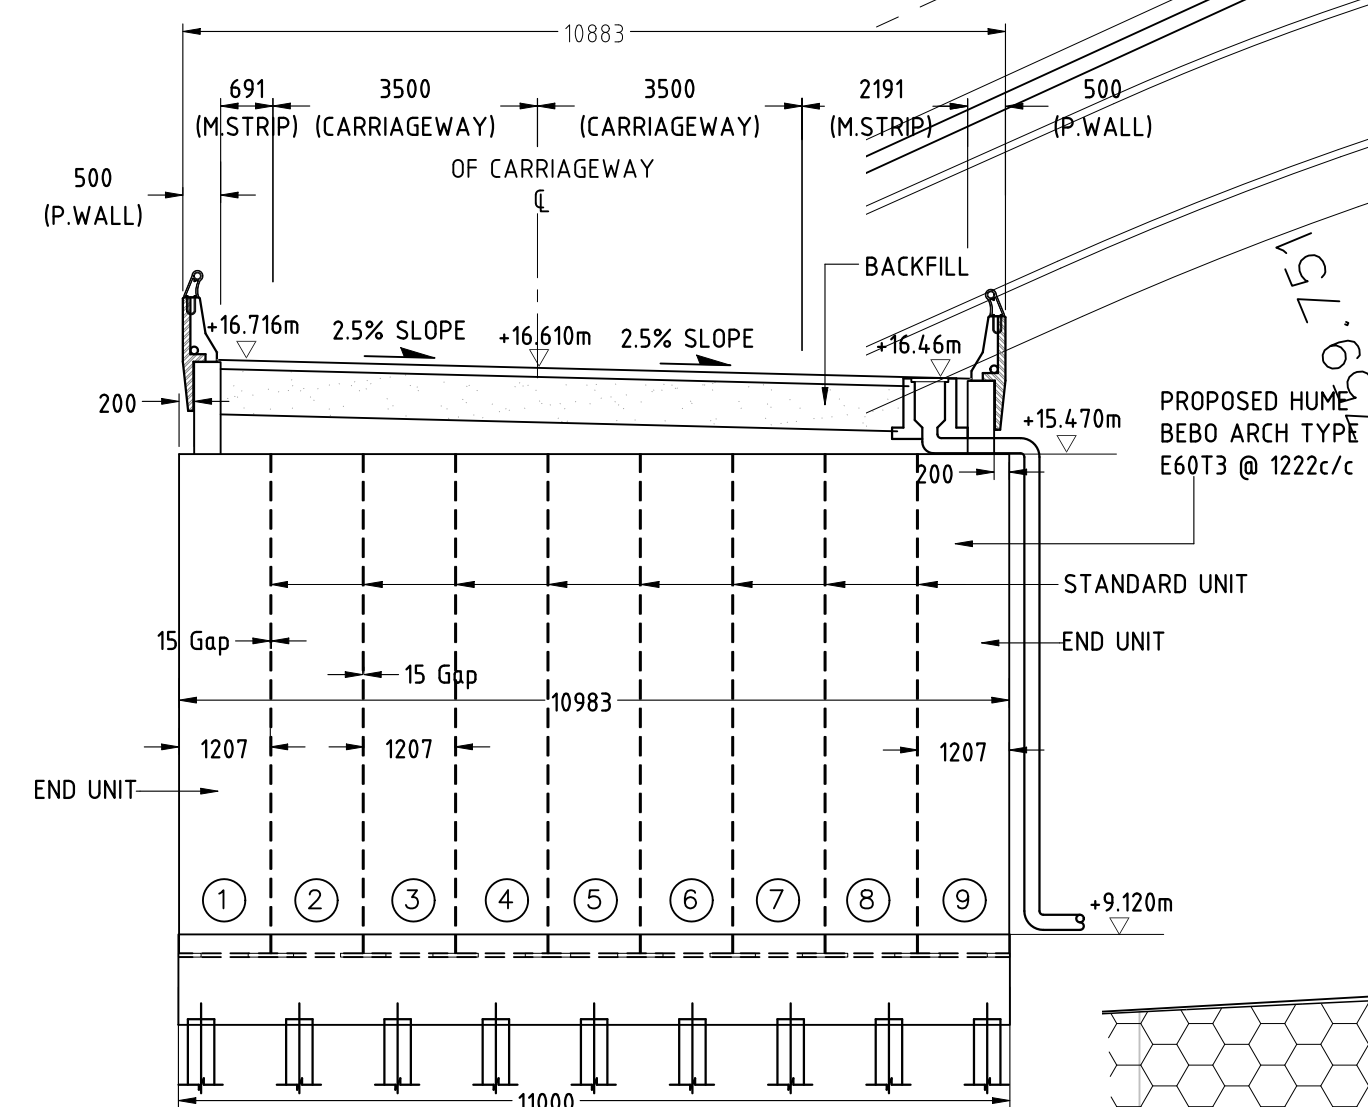

ABUTMENT FRONT
ELEVATION - VIEW 'A'

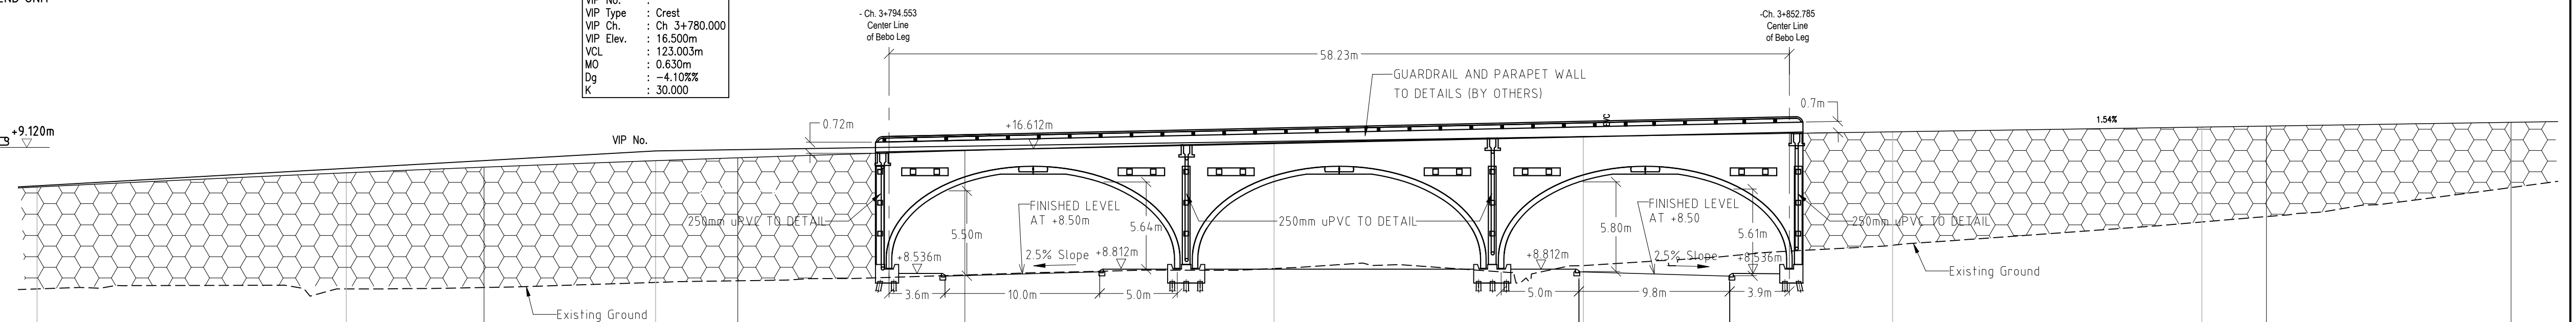

CHAINAGE	3+740.000 3+741.608	
----------	------------------------	--	--	

ELEVATION VIEW

Horizontal = 1:250
Vertical = 1:250

DATE	DESCRIPTION	REV.	CONSULTING ENGINEERS:		DRAWN BY	Din	SUPERINTENDING OFFICER:		OWNER :		PROJECT TITLE :	
			PJP PERDANA JURUTERA PERUNDING 3rd Floor, Lot 34 & 35, Block E, Damai Plaza, Phase 4, 88300 Kota Kinabalu, Sabah. P. O. Box 21251, Damai Post Office, 88770. Kota Kinabalu, Sabah.	Lead Engineer:	Design Engineer:	DESIGNED BY	Ir. Johnny C	 JABATAN KERJA RAYA SABAH	Approved by:	 KEMENTERIAN KERJA RAYA MALAYSIA	PROPOSED UPGRADING OF JALAN KOLAM, KOTA KINABALU (6 KM) INCLUDING TWO (2) FLYOVERS.	
		CHECKED BY		Ir. Lucas Lo								
		SCALE		H = Scale 1:200 V = Scale 1:200								
		DATE		January . 2019								
											DRAWING TITLE :	
											DRAWING NO.	REV.
											PJP / P205 / S2 / BP / BEBO / 02	