


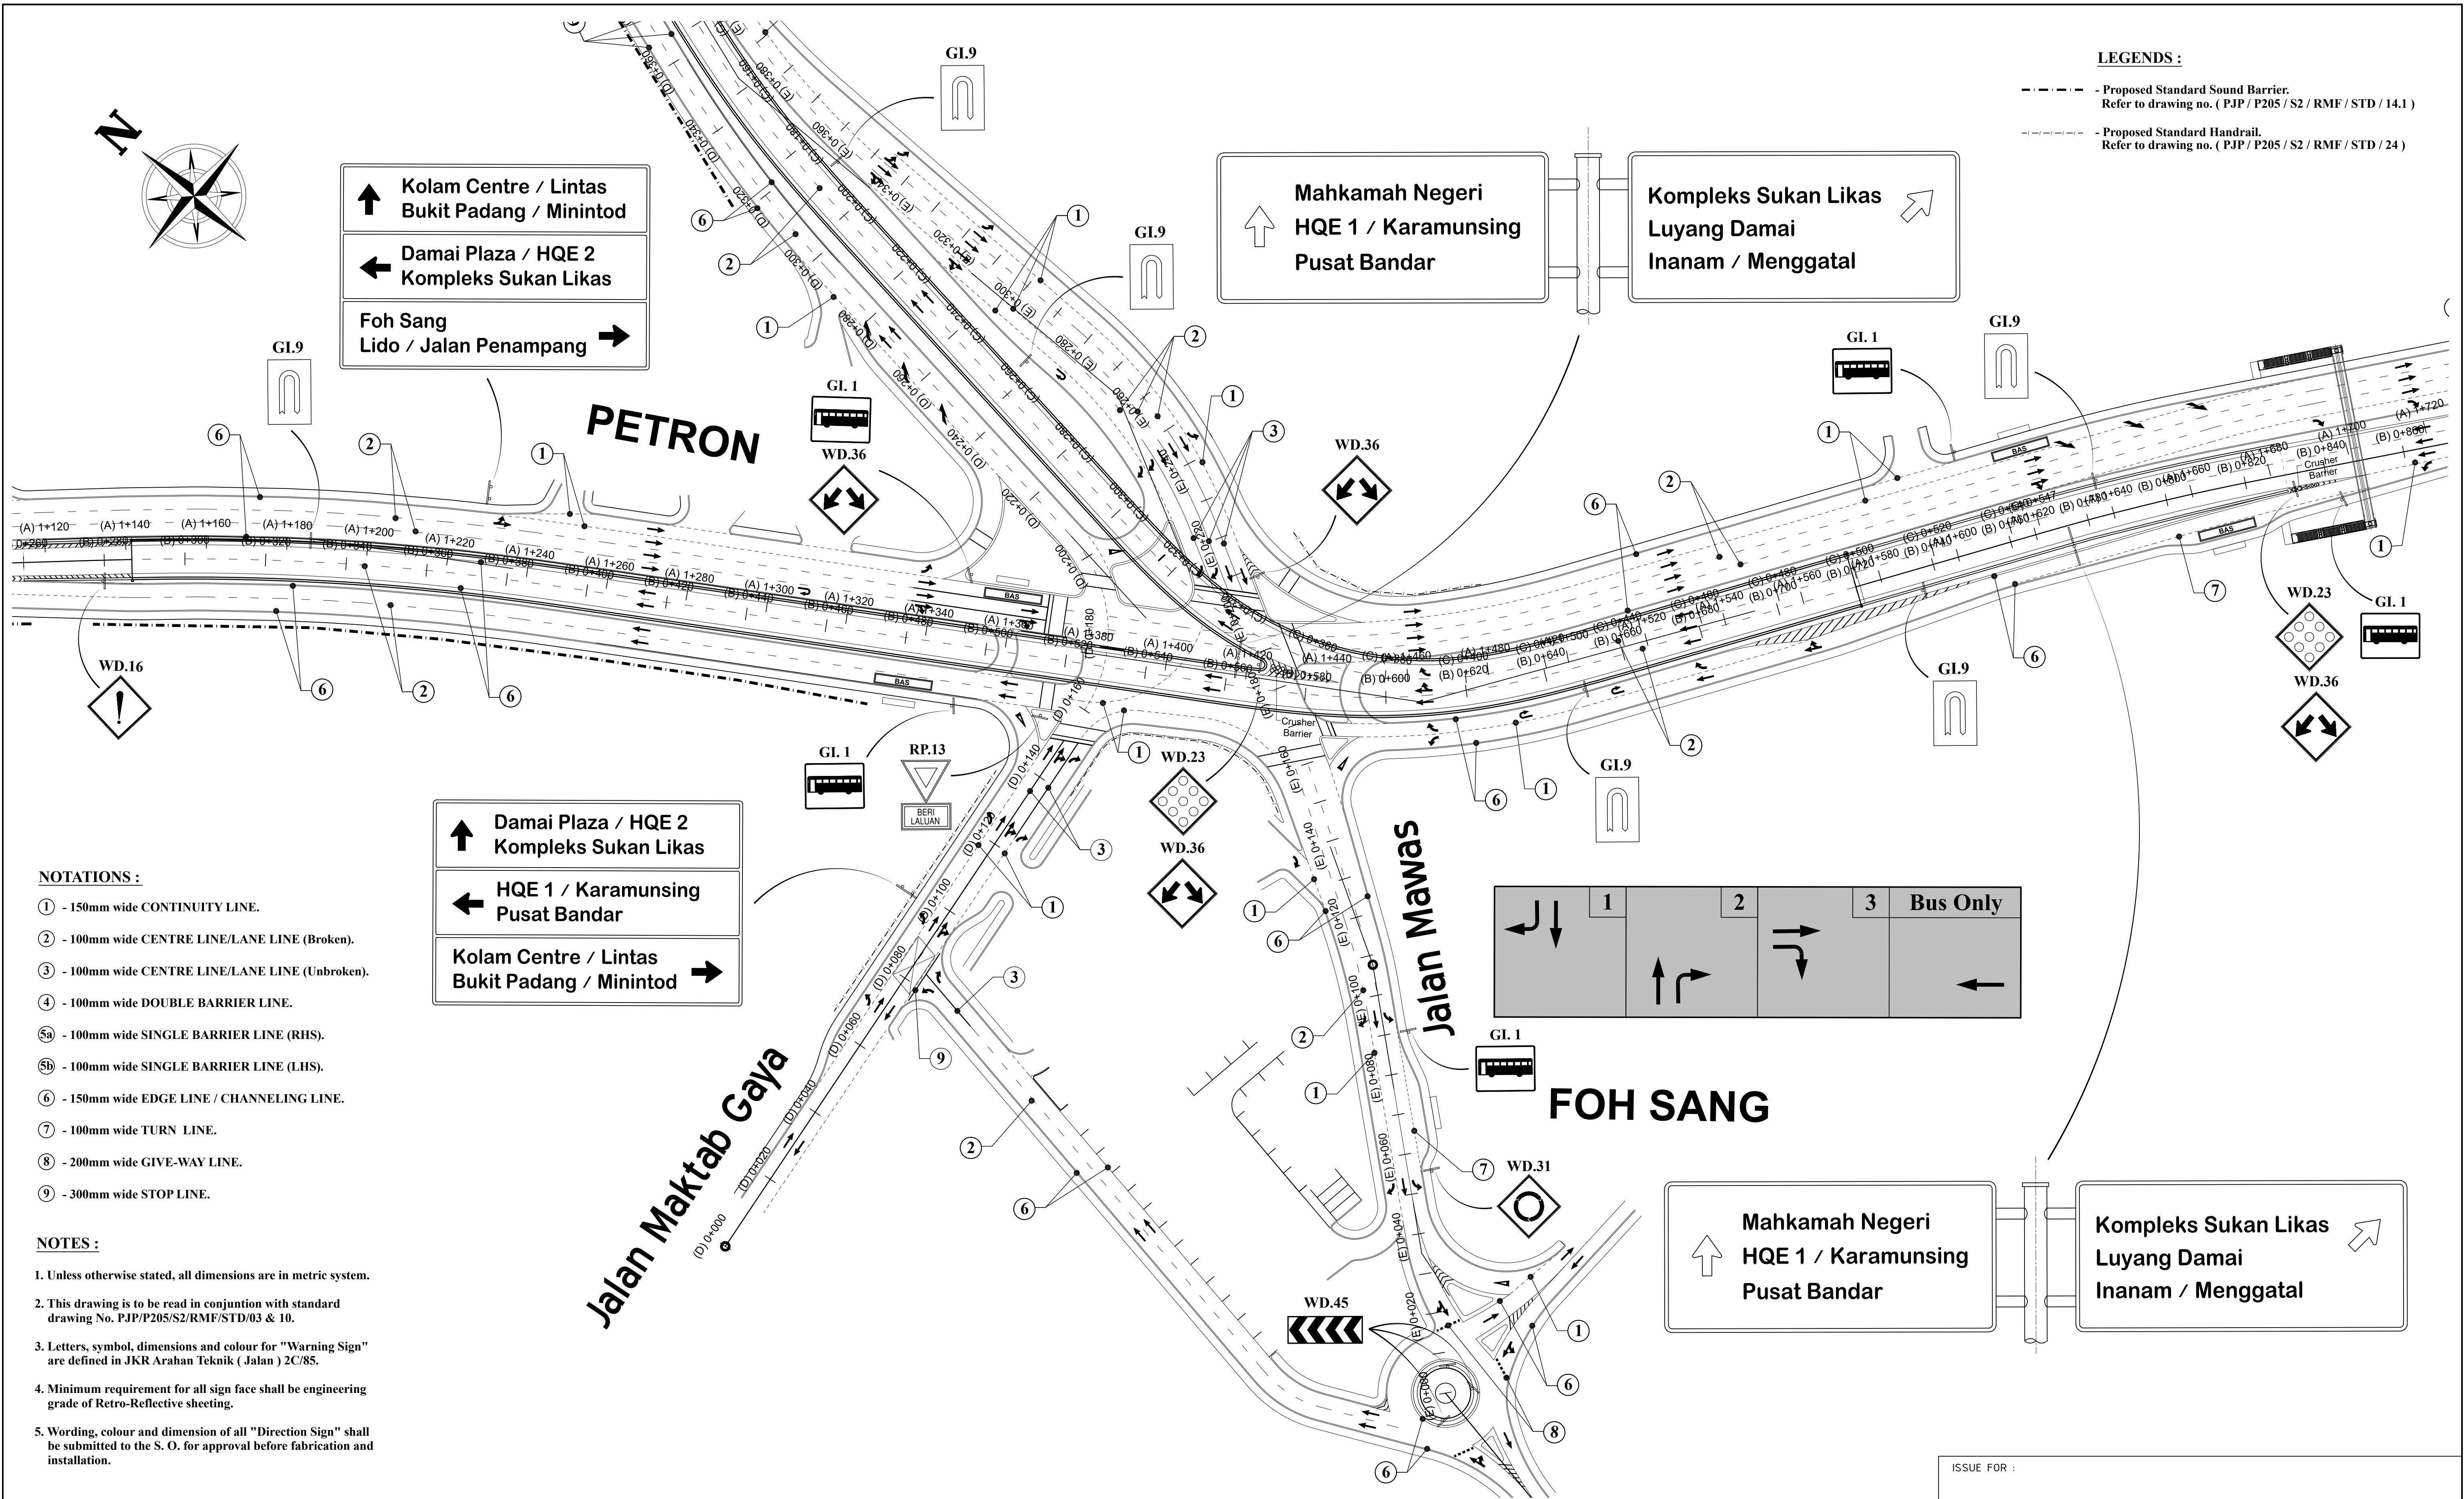

DATE	DESCRIPTION	REV.

CONSULTING ENGINEERS:		DRAWN BY	Jonathan Abah
Lead Engineer:		DESIGNED BY	George Chin
Design Engineer:		CHECKED BY	Ir. Lucas Lo
SCALE		1 : 750 (A1)	
DATE		January 2019	

SUPERINTENDING OFFICER:		OWNER :
Approved by:		
PENGARAH KERJA RAYA		

ISSUE FOR :	
PROJECT TITLE :	
DRAWING TITLE :	
DRAWING NO.	REV.

PJP
PERDANA JURUTERA PERUNDING
3rd Floor, Lot 34 & 35, Block E, Damai Plaza,
Phase 4, 88300, Kota Kinabalu,
P.O. Box No. 21251, Damai Post Office,
88770, Kota Kinabalu, SABAH, MALAYSIA.

JKR
SABAH
JABATAN KERJA RAYA
SABAH

**KEMENTERIAN
KERJA RAYA
MALAYSIA**

PROPOSED UPGRADING OF JALAN KOLAM,
KOTA KINABALU (6 KM) INCLUDING TWO (2) FLYOVERS.

PROPOSED ROAD MARKING AND SIGNAGES

PJP / P205 / S2 / RF / 04