


NOTATIONS :

- ① - 150mm wide CONTINUITY LINE.
- ② - 100mm wide CENTRE LINE/LANE LINE (Broken).
- ③ - 100mm wide CENTRE LINE/LANE LINE (Unbroken).
- ④ - 100mm wide DOUBLE BARRIER LINE.
- ⑤a - 100mm wide SINGLE BARRIER LINE (RHS).
- ⑤b - 100mm wide SINGLE BARRIER LINE (LHS).
- ⑥ - 150mm wide EDGE LINE / CHANNELING LINE.
- ⑦ - 100mm wide TURN LINE.
- ⑧ - 200mm wide GIVE-WAY LINE.
- ⑨ - 300mm wide STOP LINE.

NOTES :


- Unless otherwise stated, all dimensions are in metric system.
- This drawing is to be read in conjunction with standard drawing No. PJP/P205/S1(PH.2)/RMF/STD/03 & 10.
- Letters, symbol, dimensions and colour for "Warning Sign" are defined in JKR Arahan Teknik (Jalan) 2C/85.
- Minimum requirement for all sign face shall be engineering grade of Retro-Reflective sheeting.
- Wording, colour and dimension of all "Direction Sign" shall be submitted to the S. O. for approval before fabrication and installation.

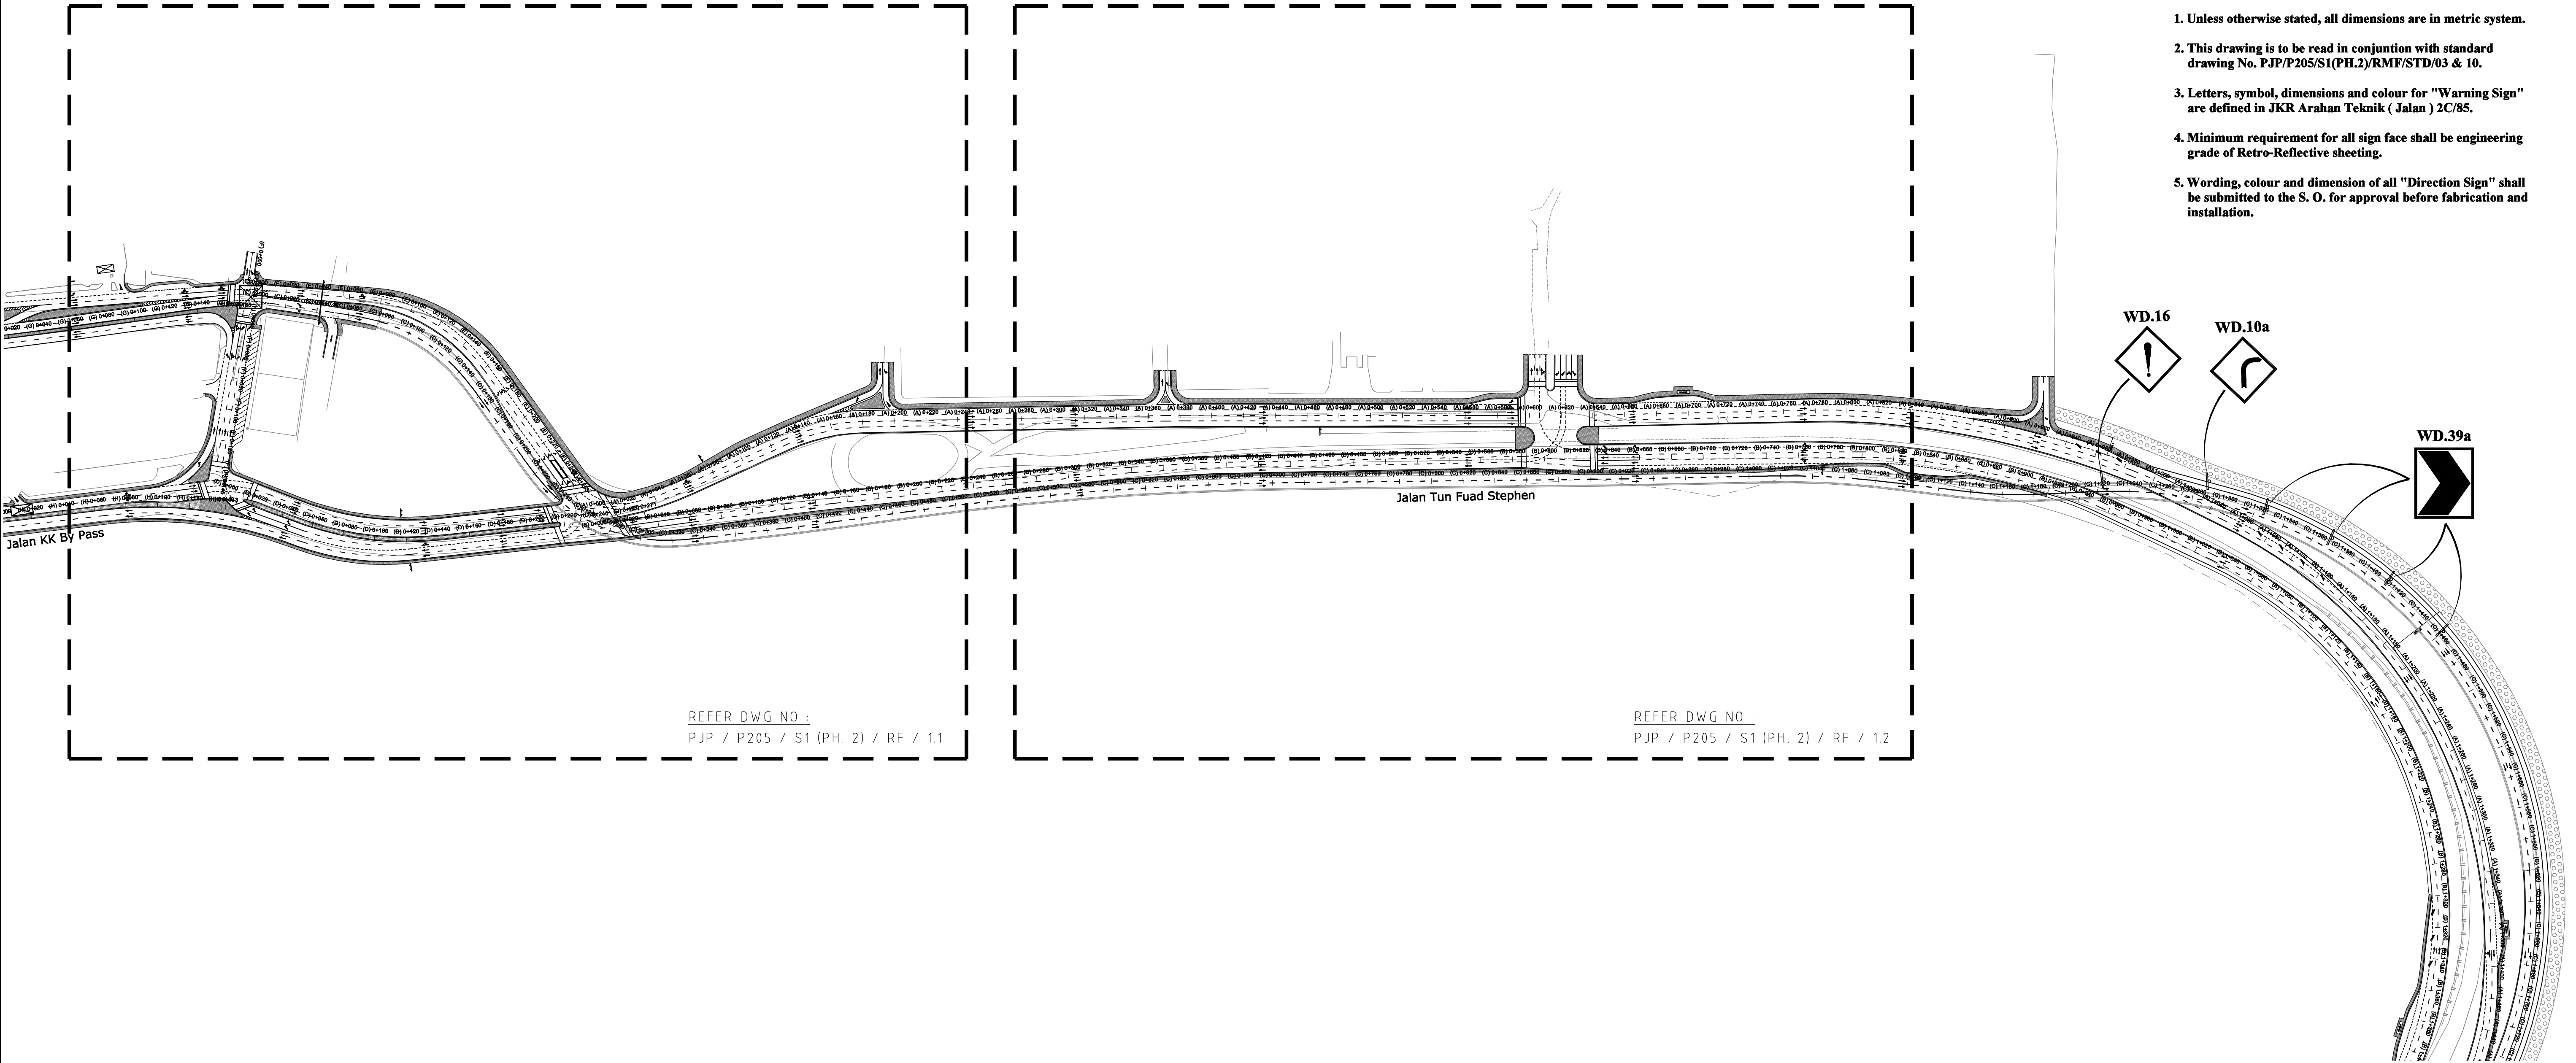

REFER DWG NO :
PJP / P205 / S1 (PH. 2) / RF / 1.1

REFER DWG NO :
PJP / P205 / S1 (PH. 2) / RF / 1.2

			ISSUE FOR :		DATE :								
DATE	DESCRIPTION	REV.	CONSULTING ENGINEERS:		SUPERINTENDING OFFICER:								
			Lead Engineer:	Design Engineer:	OWNER :								
			PJP PERDANA JURUTERA PERUNDING 3rd Floor, Lot 34 & 35, Block E, Damai Plaza, Phase 4, 88300. Kota Kinabalu. P. O. Box No. 2125/1, Damai Post Office, 88770. Kota Kinabalu, SABAH, MALAYSIA .	Lead Engineer:	Design Engineer:	DRAWN BY	Jonathan Abah	JKR SABAH JABATAN KERJA RAYA SABAH Approved by: Pengarah Kerja Raya	 KEMENTERIAN KERJA RAYA MALAYSIA	PROJECT TITLE : MENAIKTARAF JALAN TUN FUAD (0110137), KOTA KINABALU TERMASUK PEMBAIKAN TIGA PERSIMPANGAN (PERSIMPANGAN BULATAN PERKASA, PERSIMPANGAN JALAN ISTIADAT & PERSIMPANGAN JALAN PASIR)			
											DRAWING TITLE : PROPOSED ROAD MARKING AND SIGNAGES		
											DRAWING NO.	PJP / P205 / S1 (PH. 2) / RF / 01	REV.

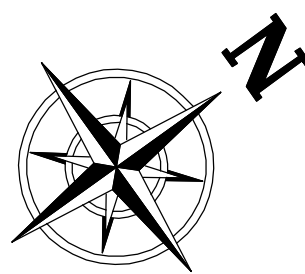


NOTATIONS :


- 1 - 150mm wide CONTINUITY LINE.
- 2 - 100mm wide CENTRE LINE/LANE LINE (Broken).
- 3 - 100mm wide CENTRE LINE/LANE LINE (Unbroken).
- 4 - 100mm wide DOUBLE BARRIER LINE.
- 5a - 100mm wide SINGLE BARRIER LINE (RHS).
- 5b - 100mm wide SINGLE BARRIER LINE (LHS).
- 6 - 150mm wide EDGE LINE / CHANNELING LINE.
- 7 - 100mm wide TURN LINE.
- 8 - 200mm wide GIVE-WAY LINE.
- 9 - 300mm wide STOP LINE.

NOTES :

1. Unless otherwise stated, all dimensions are in metric system.
2. This drawing is to be read in conjunction with standard drawing No. PJP/P205/S1(PH.2)/RMF/STD/03 & 10.
3. Letters, symbol, dimensions and colour for "Warning Sign" are defined in JKR Arahan Teknik (Jalan) 2C/85.
4. Minimum requirement for all sign face shall be engineering grade of Retro-Reflective sheeting.
5. Wording, colour and dimension of all "Direction Sign" shall be submitted to the S. O. for approval before fabrication and installation.

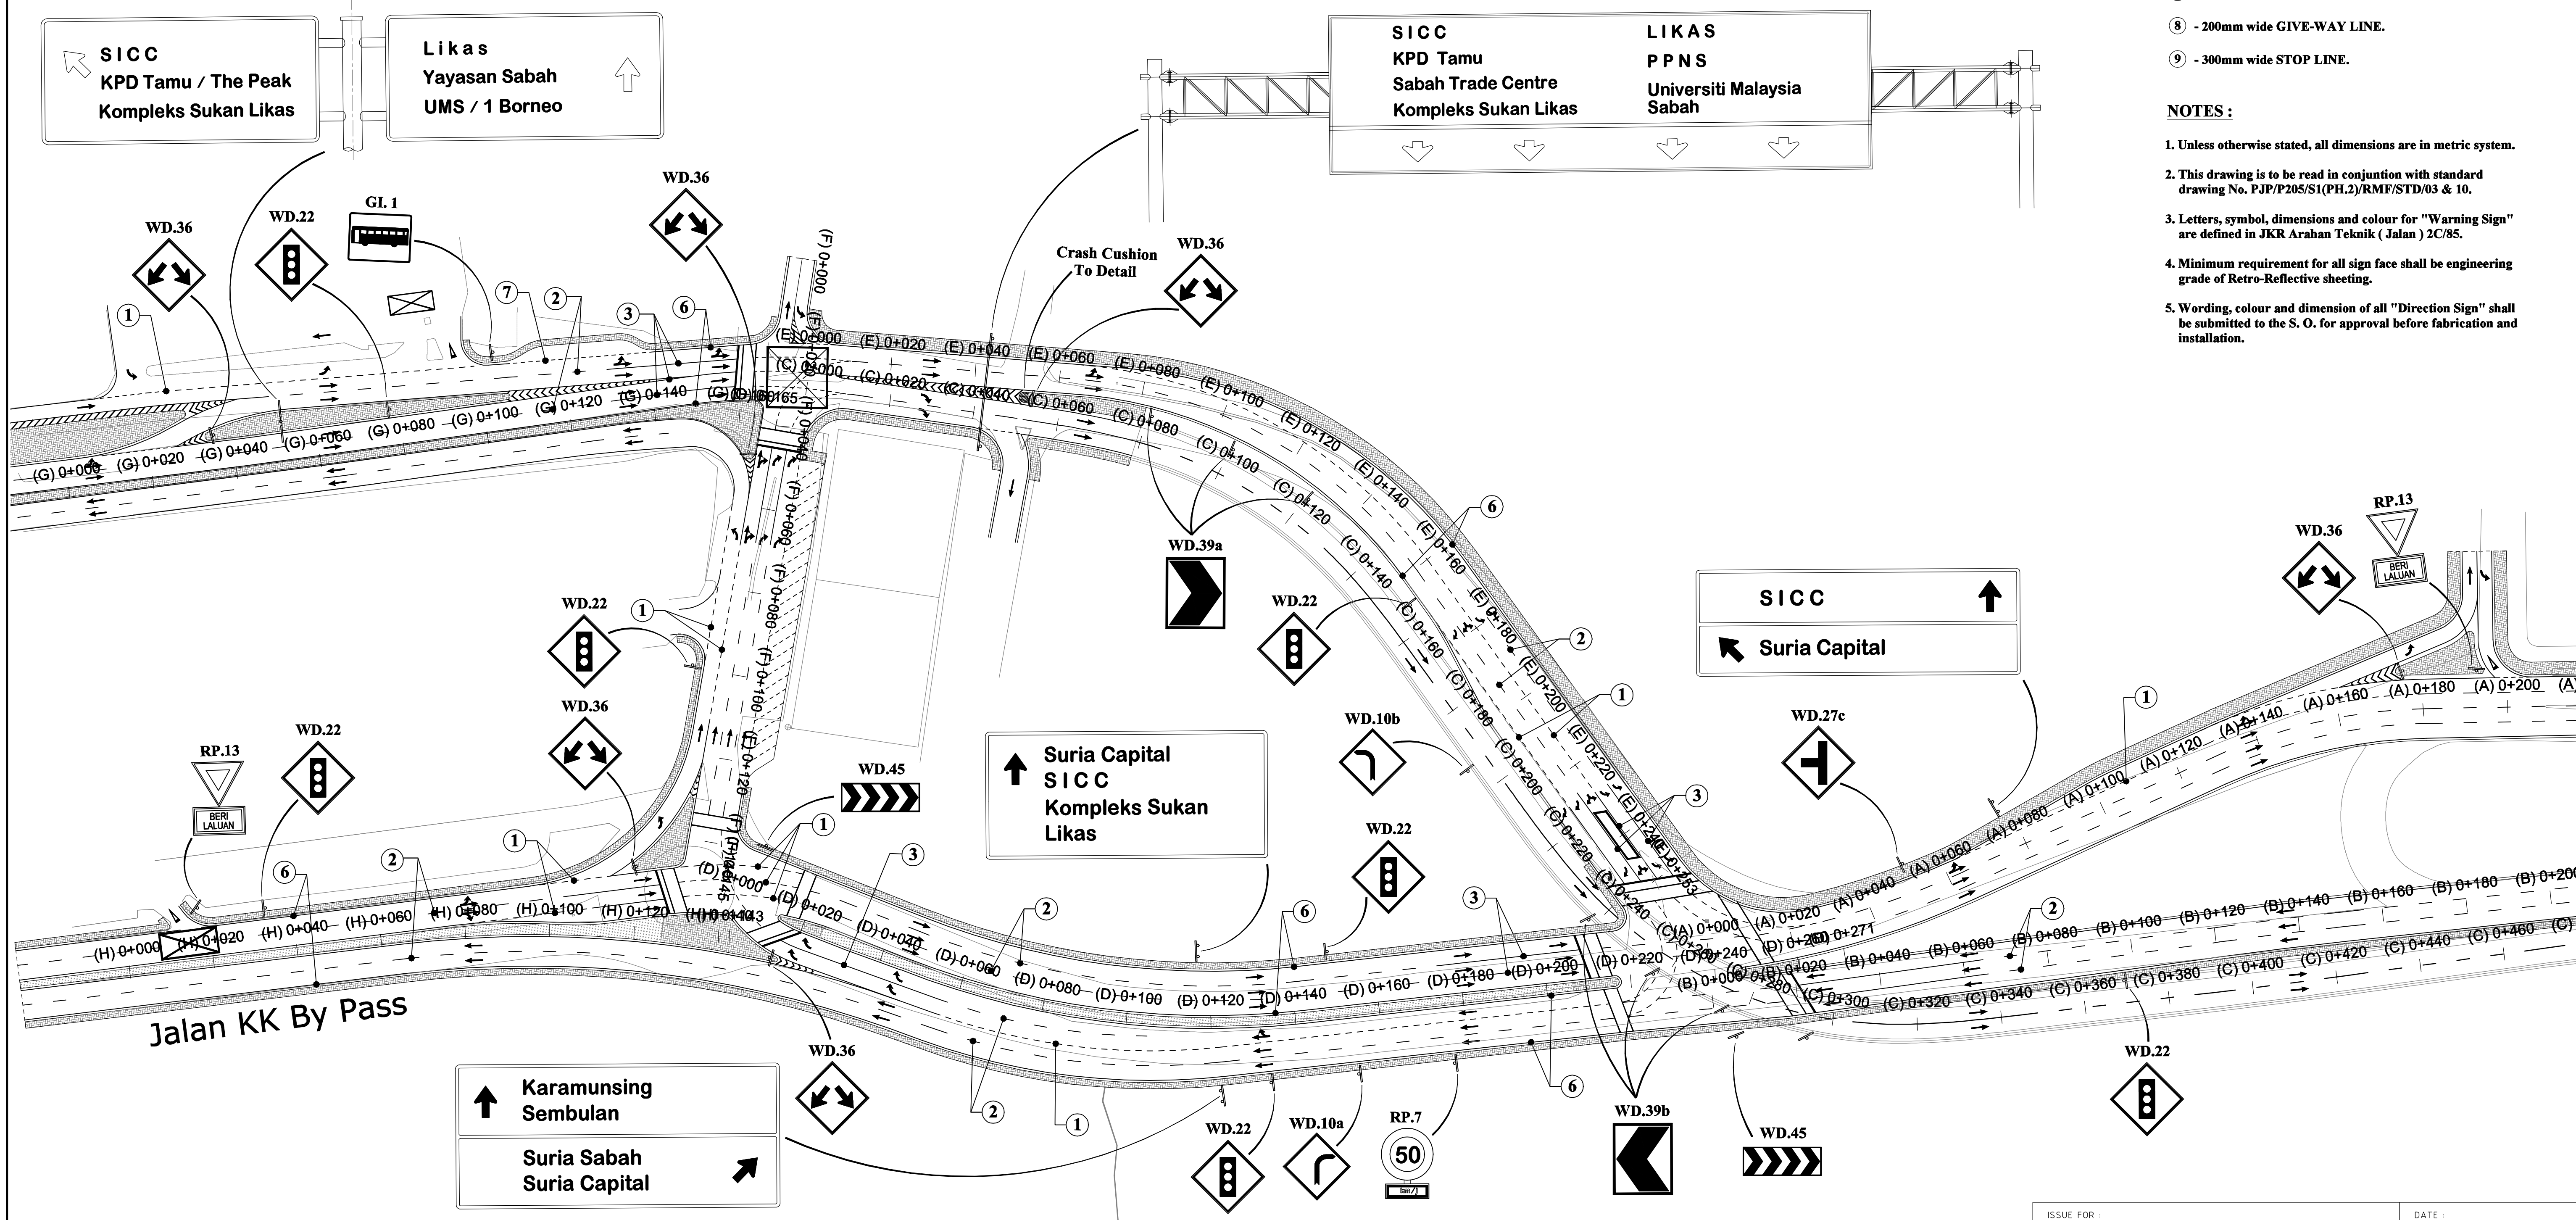


DATE			DESCRIPTION		REV.	CONSULTING ENGINEERS:		DRAWN BY		SUPERINTENDING OFFICER:		OWNER :		PROJECT TITLE :	
						PJP		DESIGNED BY		JKR				MENAIKTARAF JALAN TUN FUAD (0110137), KOTA KINABALU	
						3rd Floor, Lot 34 & 35, Block E, Damai Plaza, Phase 4, 88300, Kota Kinabalu, P. O. Box No. 21251, Damai Post Office, 88770, Kota Kinabalu, SABAH, MALAYSIA.		CHECKED BY		Approved by:		KEMENTERIAN KERJA RAYA MALAYSIA		TERMASUK PEMBAIKAN TIGA PERSIMPANGAN (PERSIMPANGAN BULATAN PERKASA, PERSIMPANGAN JALAN ISTIADAT & PERSIMPANGAN JALAN PASIR)	
						Lead Engineer:		SCALE		JABATAN KERJA RAYA SABAH				DRAWING TITLE :	
						Design Engineer:		DATE		Pengaruh Kerja Raya				PROPOSED ROAD MARKING AND SIGNAGES	
								May 2018						DRAWING NO.	
														PJP / P205 / S1 (PH. 2) / RF / 1.1	
														REV.	

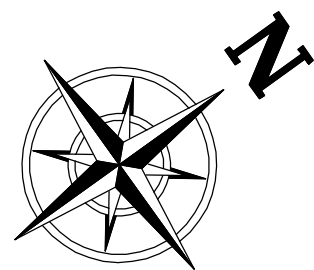

- NOTATIONS :**
- ① - 150mm wide CONTINUITY LINE.
 - ② - 100mm wide CENTRE LINE/LANE LINE (Broken).
 - ③ - 100mm wide CENTRE LINE/LANE LINE (Unbroken).
 - ④ - 100mm wide DOUBLE BARRIER LINE.
 - 5a - 100mm wide SINGLE BARRIER LINE (RHS).
 - 5b - 100mm wide SINGLE BARRIER LINE (LHS).
 - ⑥ - 150mm wide EDGE LINE / CHANNELING LINE.
 - ⑦ - 100mm wide TURN LINE.
 - ⑧ - 200mm wide GIVE-WAY LINE.
 - ⑨ - 300mm wide STOP LINE.

- NOTES :**
- Unless otherwise stated, all dimensions are in metric system.
 - This drawing is to be read in conjunction with standard drawing No. PJP/P205/S1(PH.2)/RMF/STD/03 & 10.
 - Letters, symbol, dimensions and colour for "Warning Sign" are defined in JKR Arahan Teknik (Jalan) 2C/85.
 - Minimum requirement for all sign face shall be engineering grade of Retro-Reflective sheeting.
 - Wording, colour and dimension of all "Direction Sign" shall be submitted to the S. O. for approval before fabrication and installation.

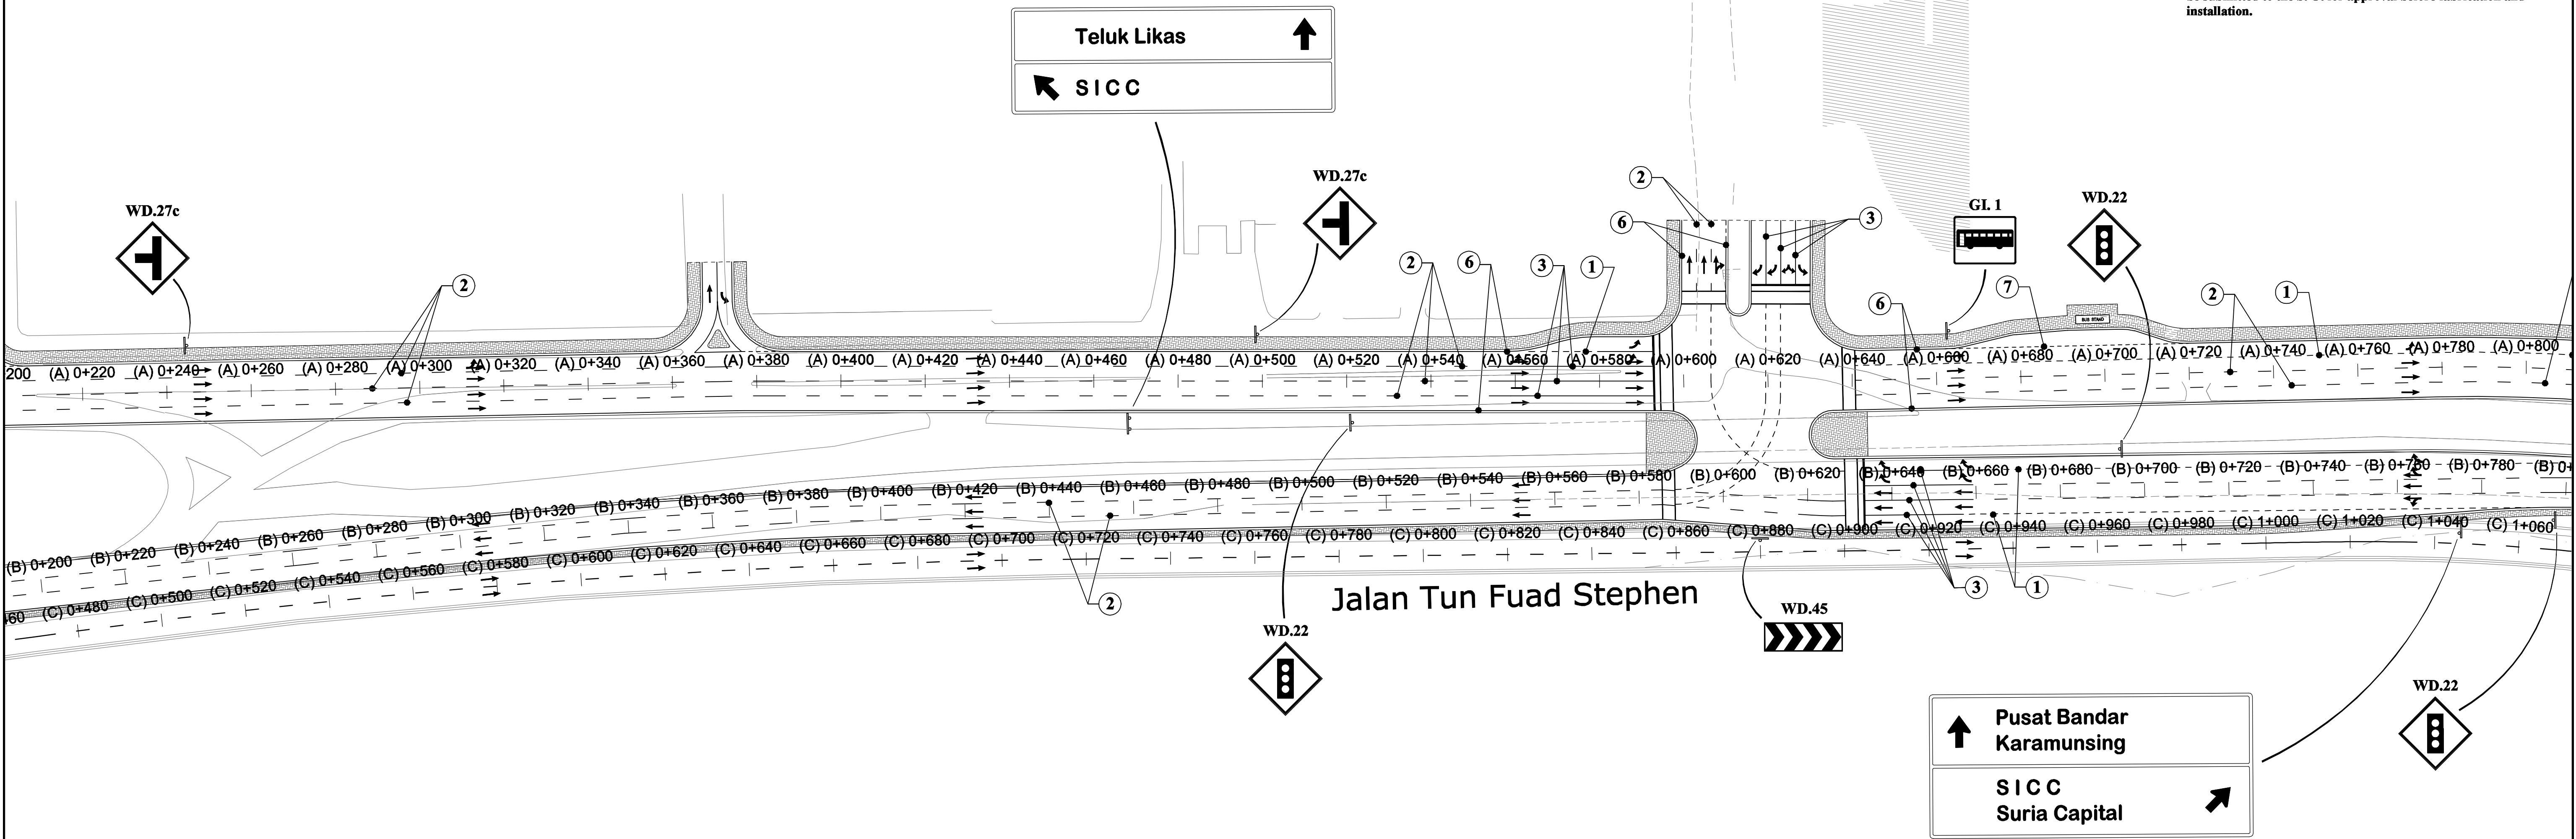

DATE			DESCRIPTION		REV.	CONSULTING ENGINEERS:		DRAWN BY		SUPERINTENDING OFFICER:		OWNER :		ISSUE FOR :		DATE :	
						PJP PERDANA JURUTERA PERUNDING 3rd Floor, Lot 34 & 35, Block E, Damai Plaza, Phase 4, 88300, Kota Kinabalu, P. O. Box No. 21251, Damai Post Office, 88770, Kota Kinabalu, SABAH, MALAYSIA.		Lead Engineer:		DESIGNED BY		 JABATAN KERJA RAYA SABAH		PROJECT TITLE :		DRAWING TITLE :	
								Design Engineer:		CHECKED BY		KEMENTERIAN KERJA RAYA MALAYSIA		MENAIKTARAF JALAN TUN FUAD (0110137), KOTA KINABALU TERMASUK PEMBAIKAN TIGA PERSIMPANGAN (PERSIMPANGAN BULATAN PERKASA, PERSIMPANGAN JALAN ISTIADAT & PERSIMPANGAN JALAN PASIR)		DRAWING NO.	
										SCALE				PROPOSED ROAD MARKING AND SIGNAGES		PJP / P205 / S1 (PH. 2) / RF / 1.2	
								DATE		1 : 750						REV.	
								May 2018									